



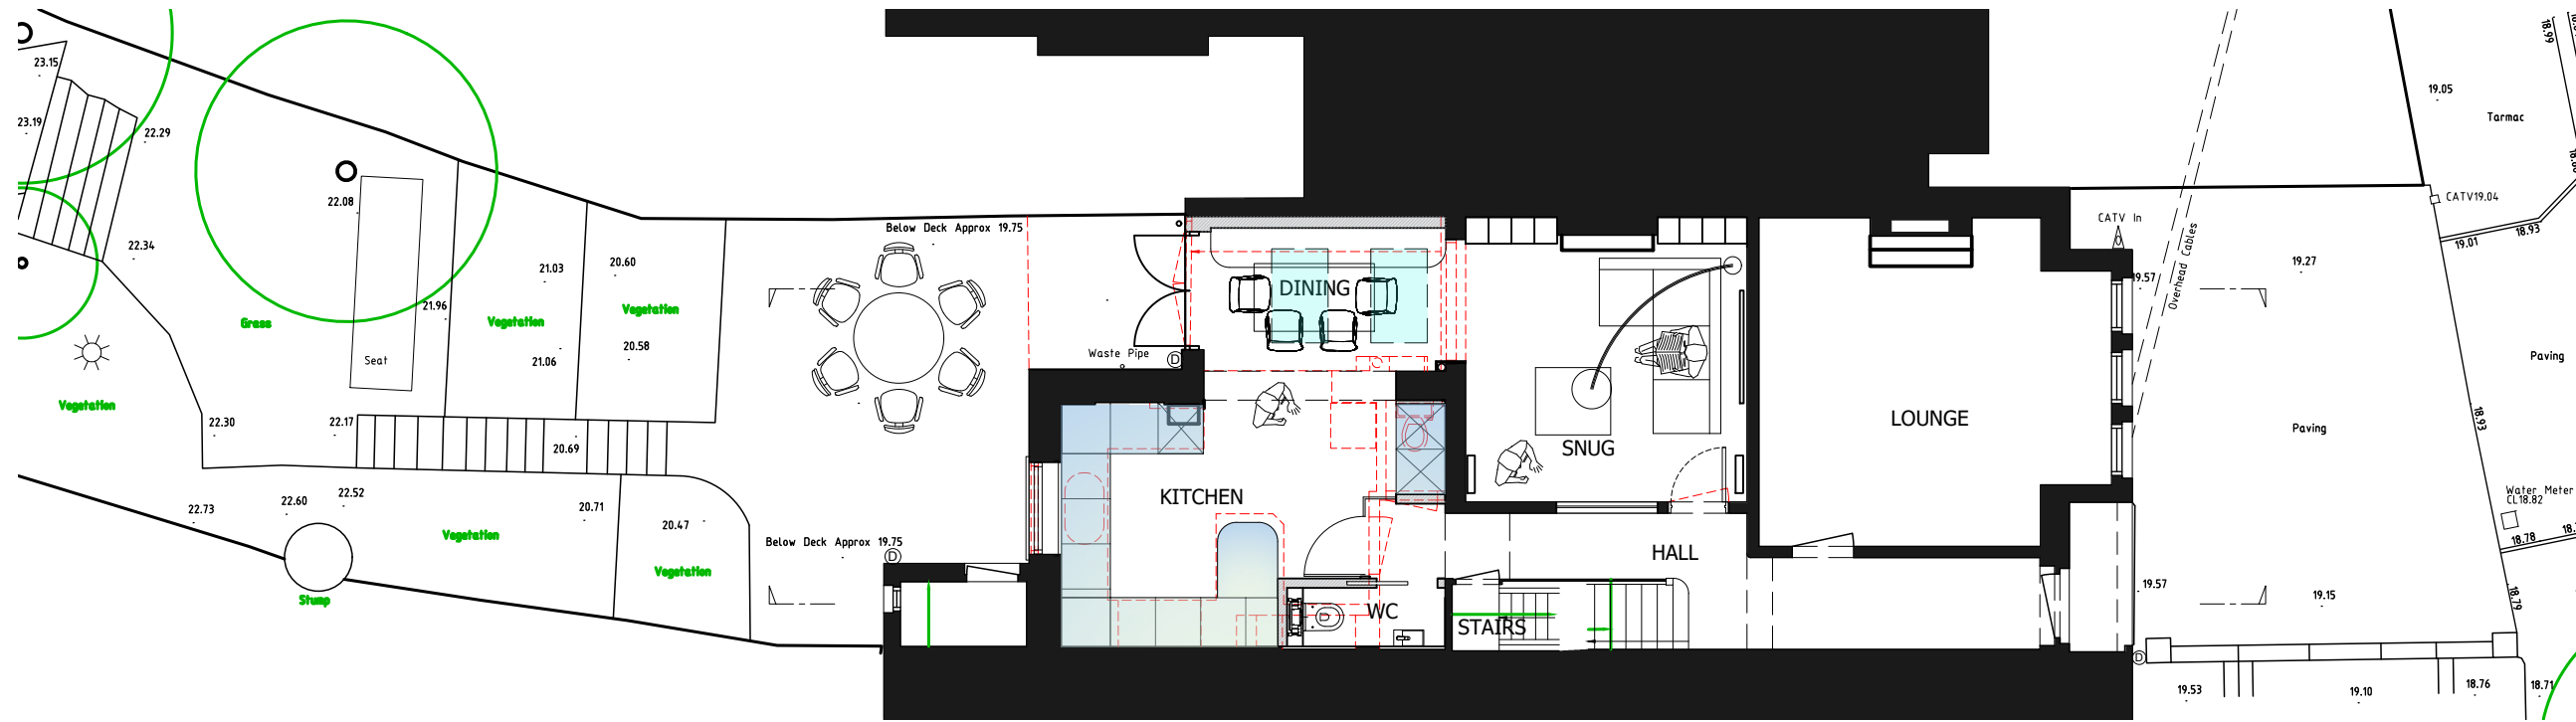


THE CONTRACTOR MUST VERIFY ALL DIMENSIONS ON SITE BEFORE MAKING SHOP DRAWINGS OR COMMENCING WORK OF ANY KIND. NO DIMENSIONS TO BE SCALED FROM THIS DRAWING.

REV.	DATE	REVISION
P1	23.10.23	first issue for comment
P2	20.12.23	updates following Client meeting
P3	21.12.23	minor amendments
P4	06.03.24	prepared for Planning

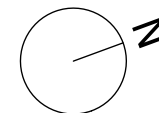


SCALE 1:100
SCALE 1:1

0m 1m 2m
0m 10mm 20mm

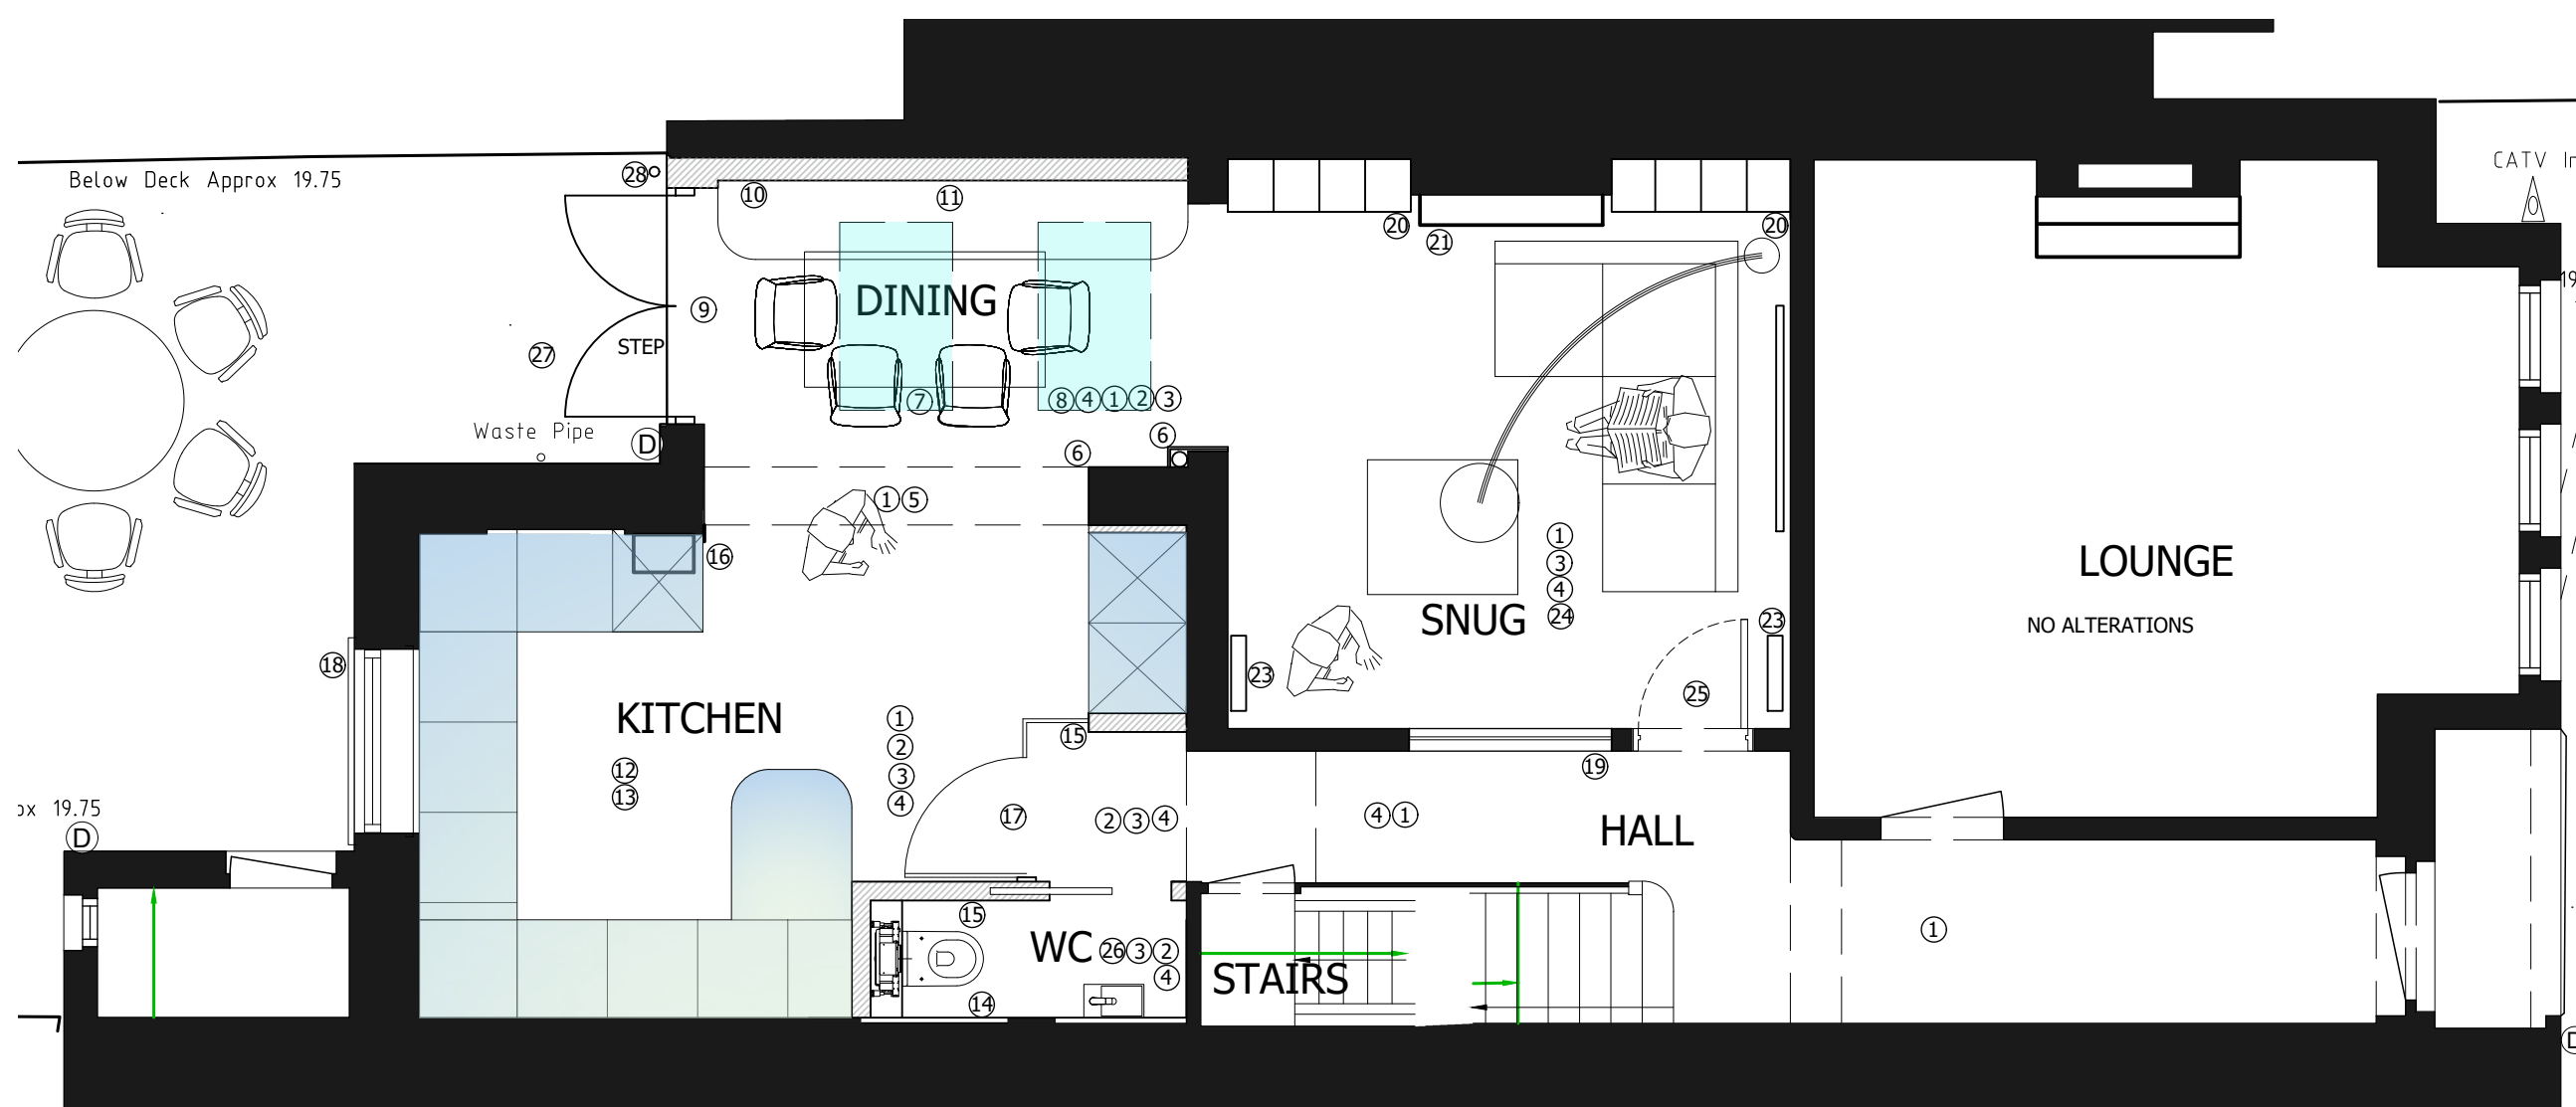

SCALE 1:50
SCALE 1:1

0m 0.5m 1m
0m 10mm 20mm

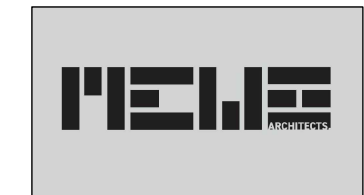

MEW ARCHITECTS Limited, Chartered Architect

PLANNING

ALL WORKS TO BE IN ACCORDANCE WITH UK BUILDING REGULATIONS AND RELEVANT BRITISH STANDARDS.
TO BE READ IN CONJUNCTION WITH ARCHITECTS SCHEDULE OF WORKS.
IF IN DOUBT PLEASE ASK.
ALL DIMENSIONS TO BE CONFIRMED BY SUPPLIERS/INSTALLERS/ BUILDER BY THEIR OWN SITE MEASURE.
DASHED RED LINES DENOTE DEMOLITION WHERE APPLICABLE.
MEASURED SURVEY COMPLETED BY JTW SURVEYS

PROJECT:
54 Whiteley Road
London
SE19 1JT

CLIENT:
Louise and Matthew McGregor

DRAWING:
PROPOSED GROUND FLOOR PLAN

DRAWING No.:
020

REV:
P4

SCALE:
DRAWN: MEW
CHECKED:

DATE: 21.10.23
DATE:

MEW architects Limited, Matt Weyham RIBA, Chartered Architect
E-mail: info@mewarchitects.com Web: www.MEWarchitects.com
©COPYRIGHT EXISTS ON THE DESIGNS AND INFORMATION SHOWN ON THIS DRAWING