
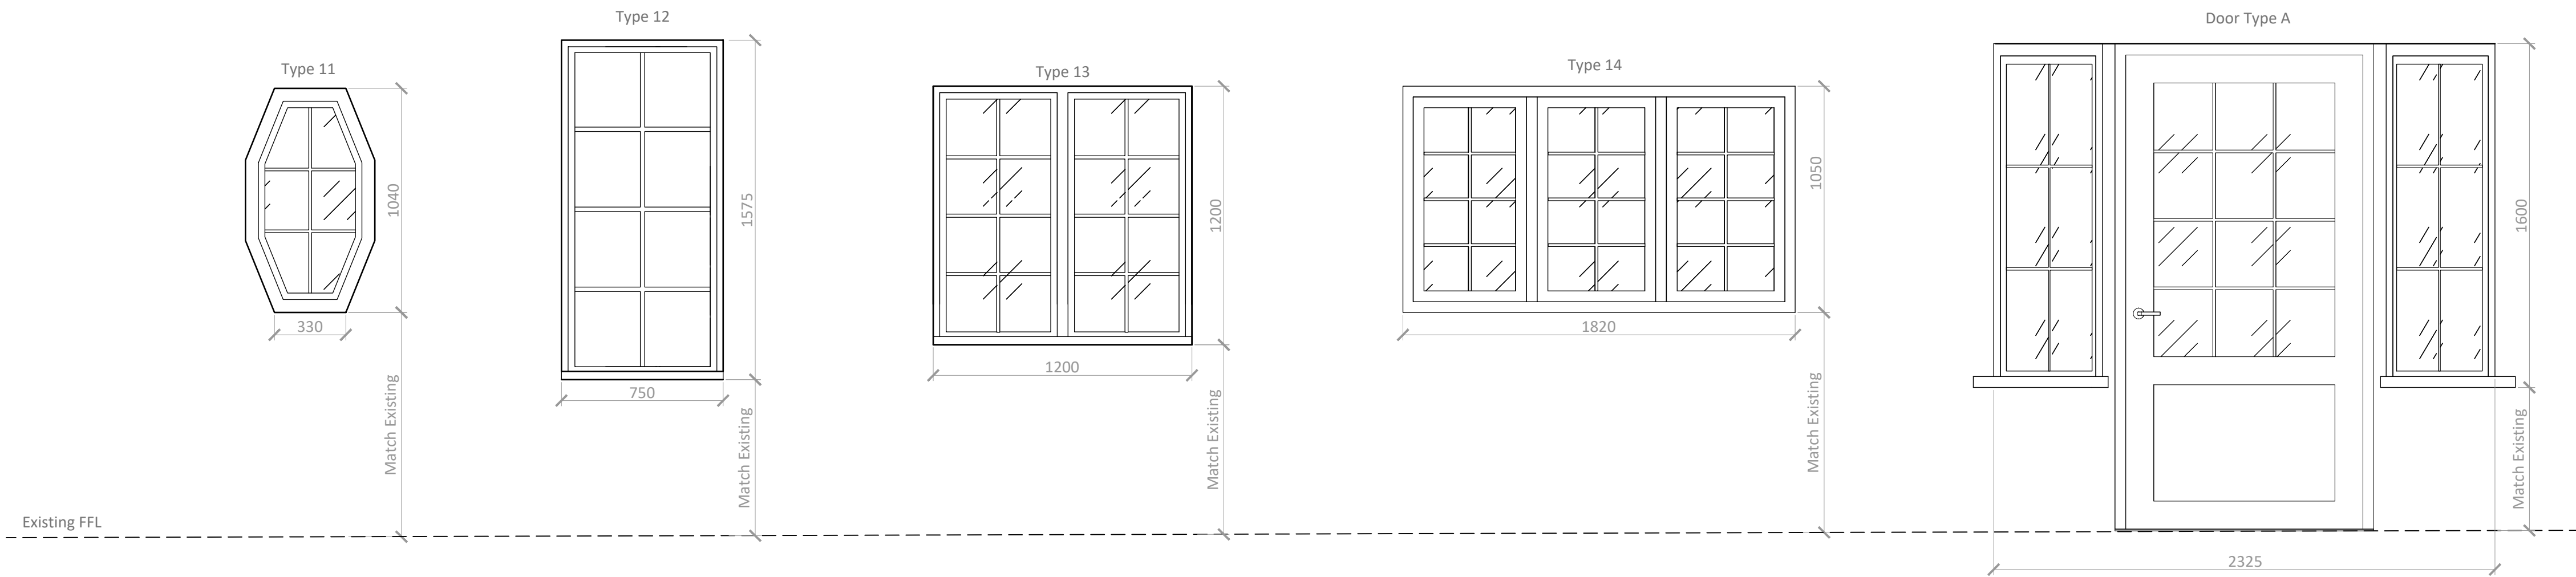
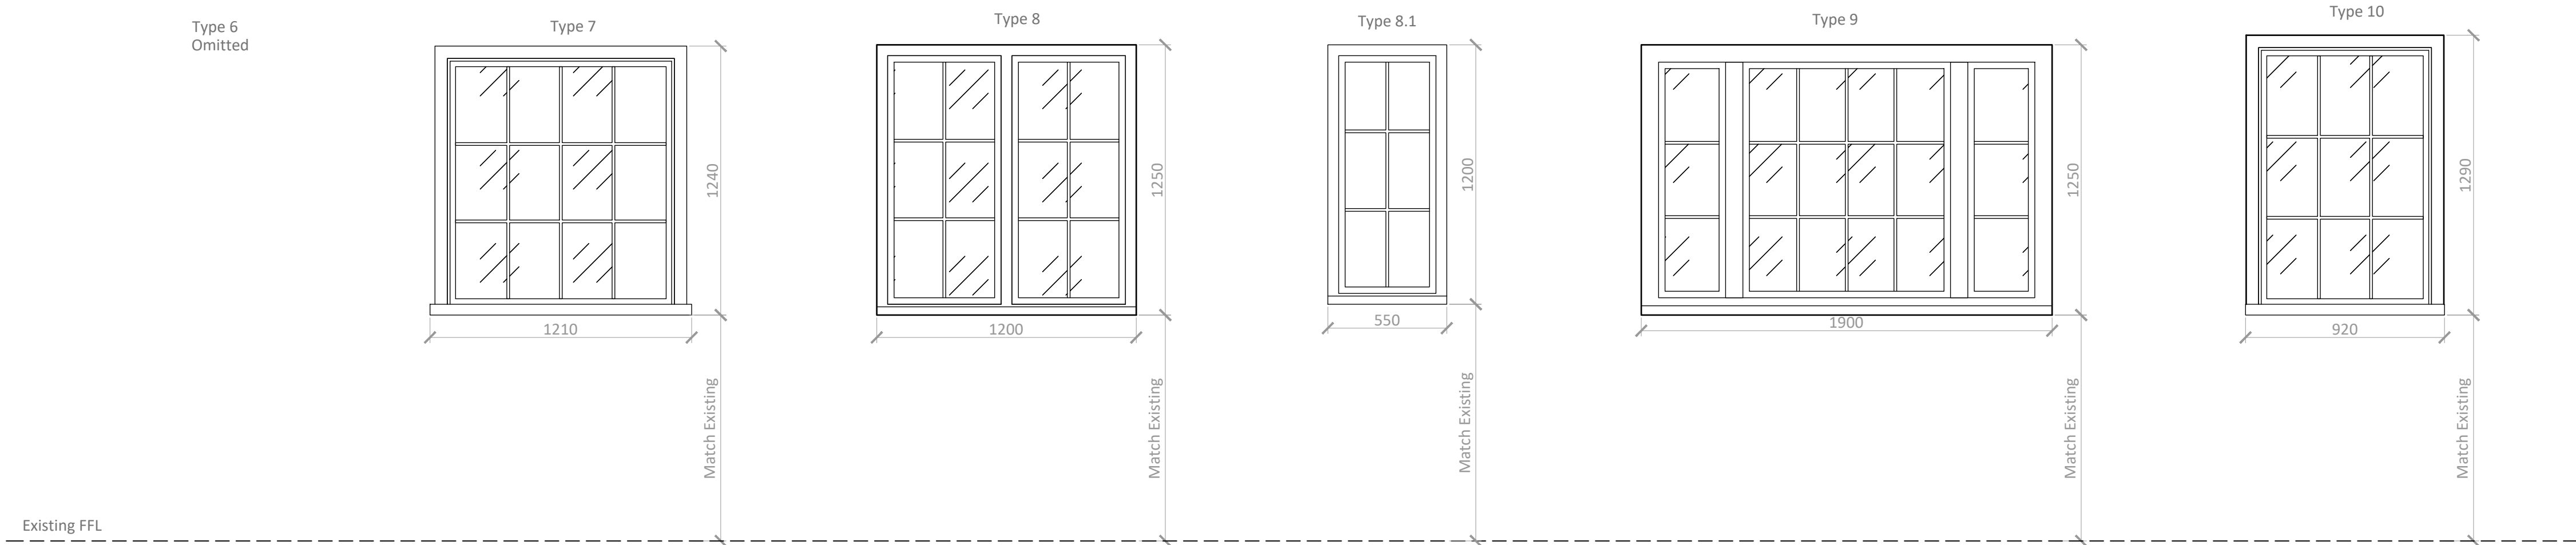


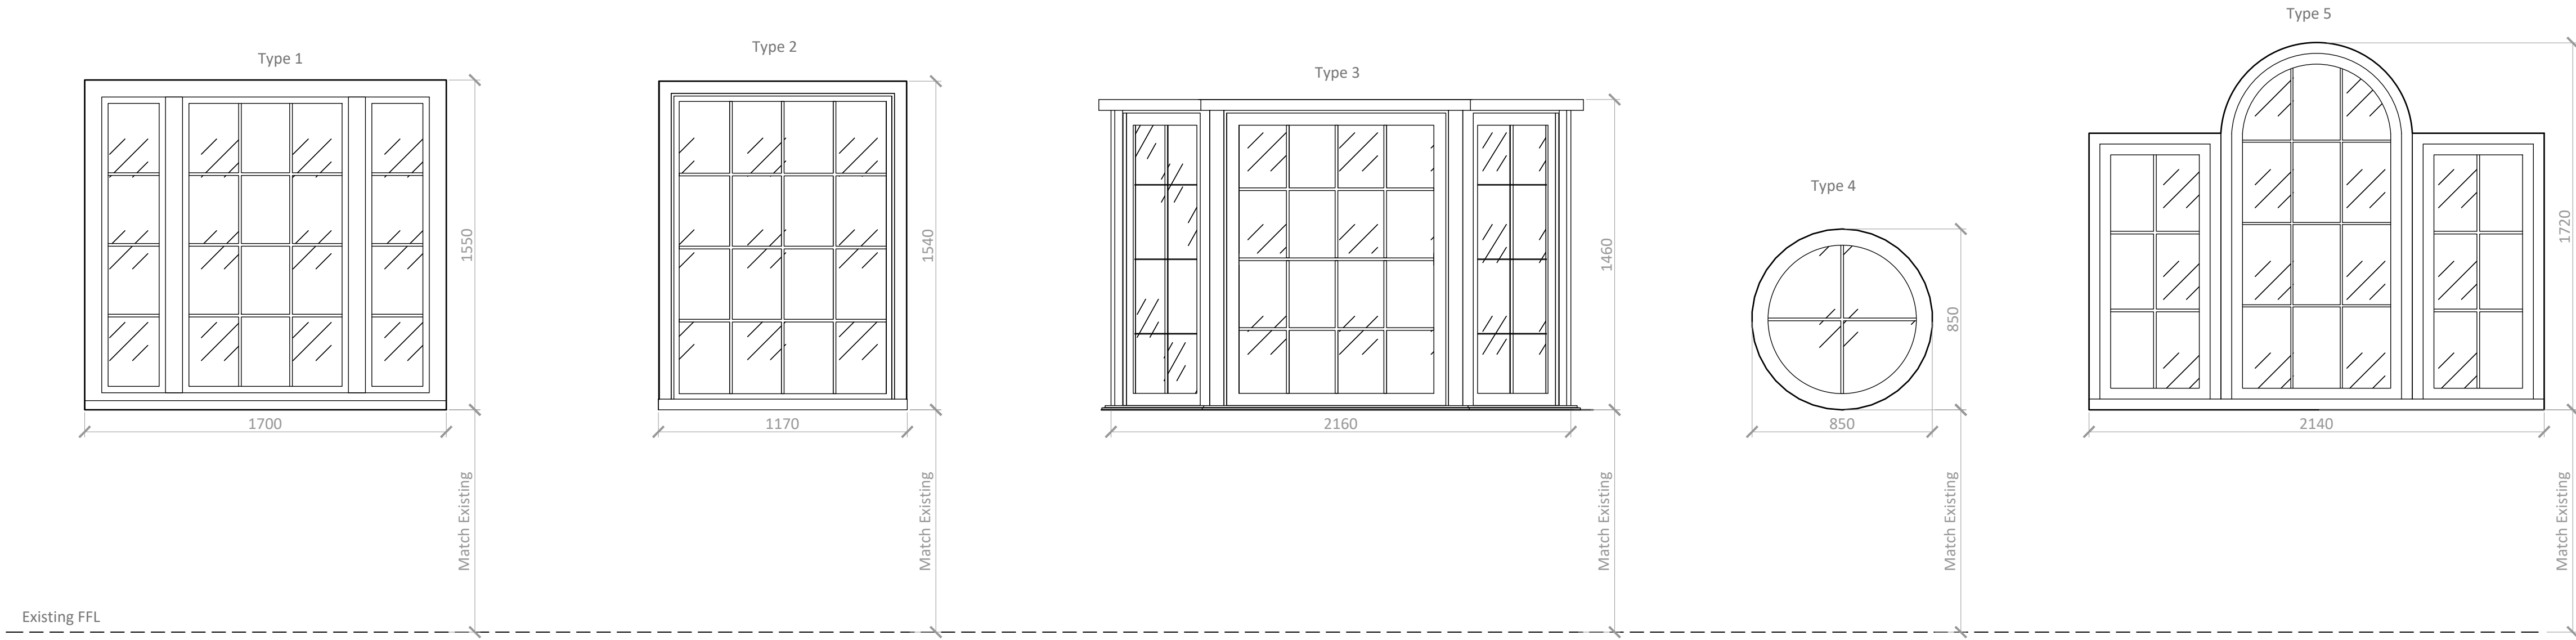

DISCLAIMER :
All dimensions and levels to be checked on site by contractor prior to preparation of shop/specialist drawings and commencement of work on site.
Do not scale from this drawing. If you scale from this drawing then you do so at your own risk. Martin Arnold Ltd will not be responsible for any implications resulting from scaling from the drawing.
This drawing and the copyrights and patents therein are the property of Martin Arnold Ltd and may not be used or reproduced without consent.
This drawing is to be read in conjunction with all relevant consultants' and/or specialist drawings and documents and any discrepancies or variations are to be notified to Martin Arnold Ltd before the affected work commences.
MA Code (for MA use only): AMB4163
Dimensions provided based on measured survey information provided by Multivista (ref: A301- A302-A303-A304)

000 240328 RC First Issue

Rev	Date	By	Description
-----	------	----	-------------

MA

MARTIN ARNOLD

ARCHITECTS

Martin Arnold Limited

4 Guntery Terrace

The Royal Arsenal

London

SE18 6SW

CLIENT :

Amber Construction

PROJECT :

Newquay House

TITLE :

Existing Windows Elevations

Purpose of Issue :

APPROVAL

Drawn : RC

Checked By : PS

Date : MARCH 2024

Scale : 1:20@A1

Dwg No : 4163-MA-E-EL-WN-DR-2240-D00