


COMMON AREAS


FLAT 1 (1bed /1 p)

FLAT 2 (2 bed / 3p)


KEY

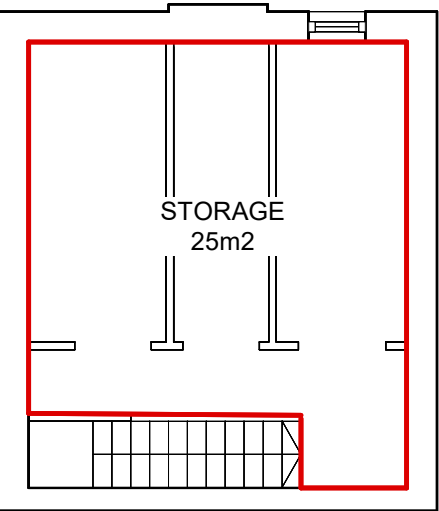


EXISTING BASEMENT PLAN

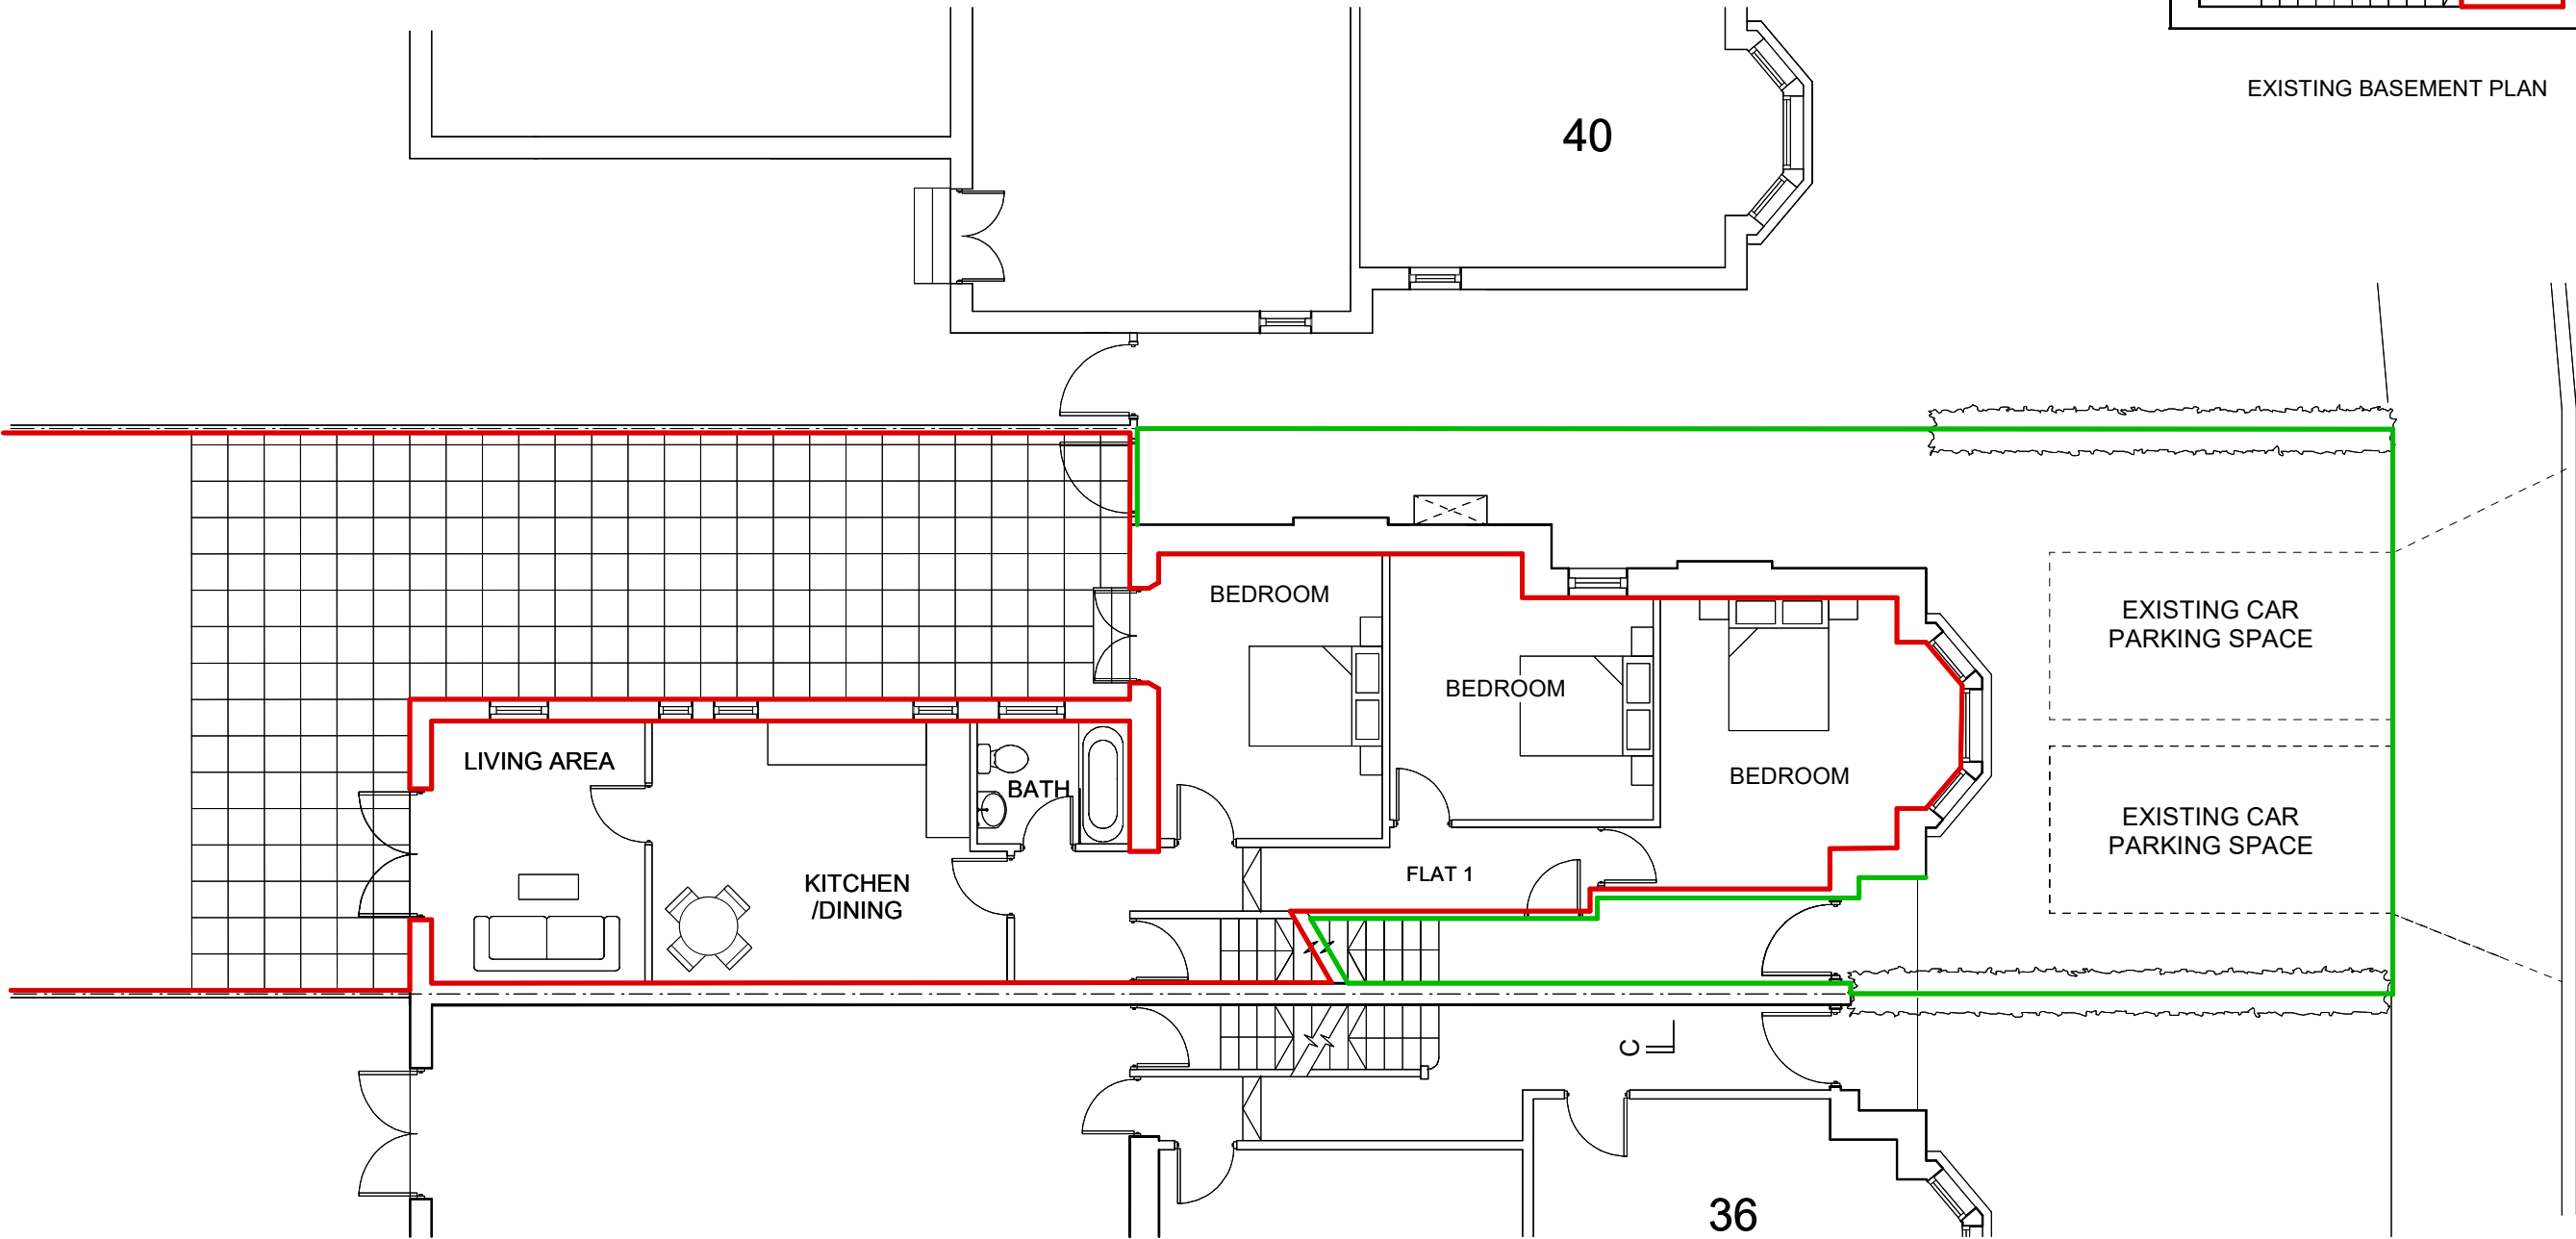


EXISTING GROUND FLOOR PLAN

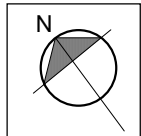



COMMON AREAS ■ FLAT 1 (1bed / 1 p) ■ FLAT 2 (2 bed / 3p) ■ KEY

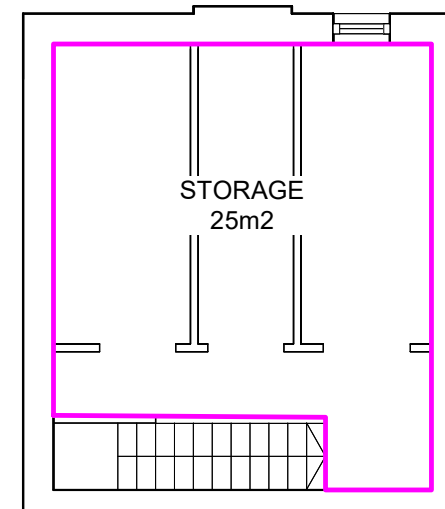


PROPOSED BASEMENT PLAN

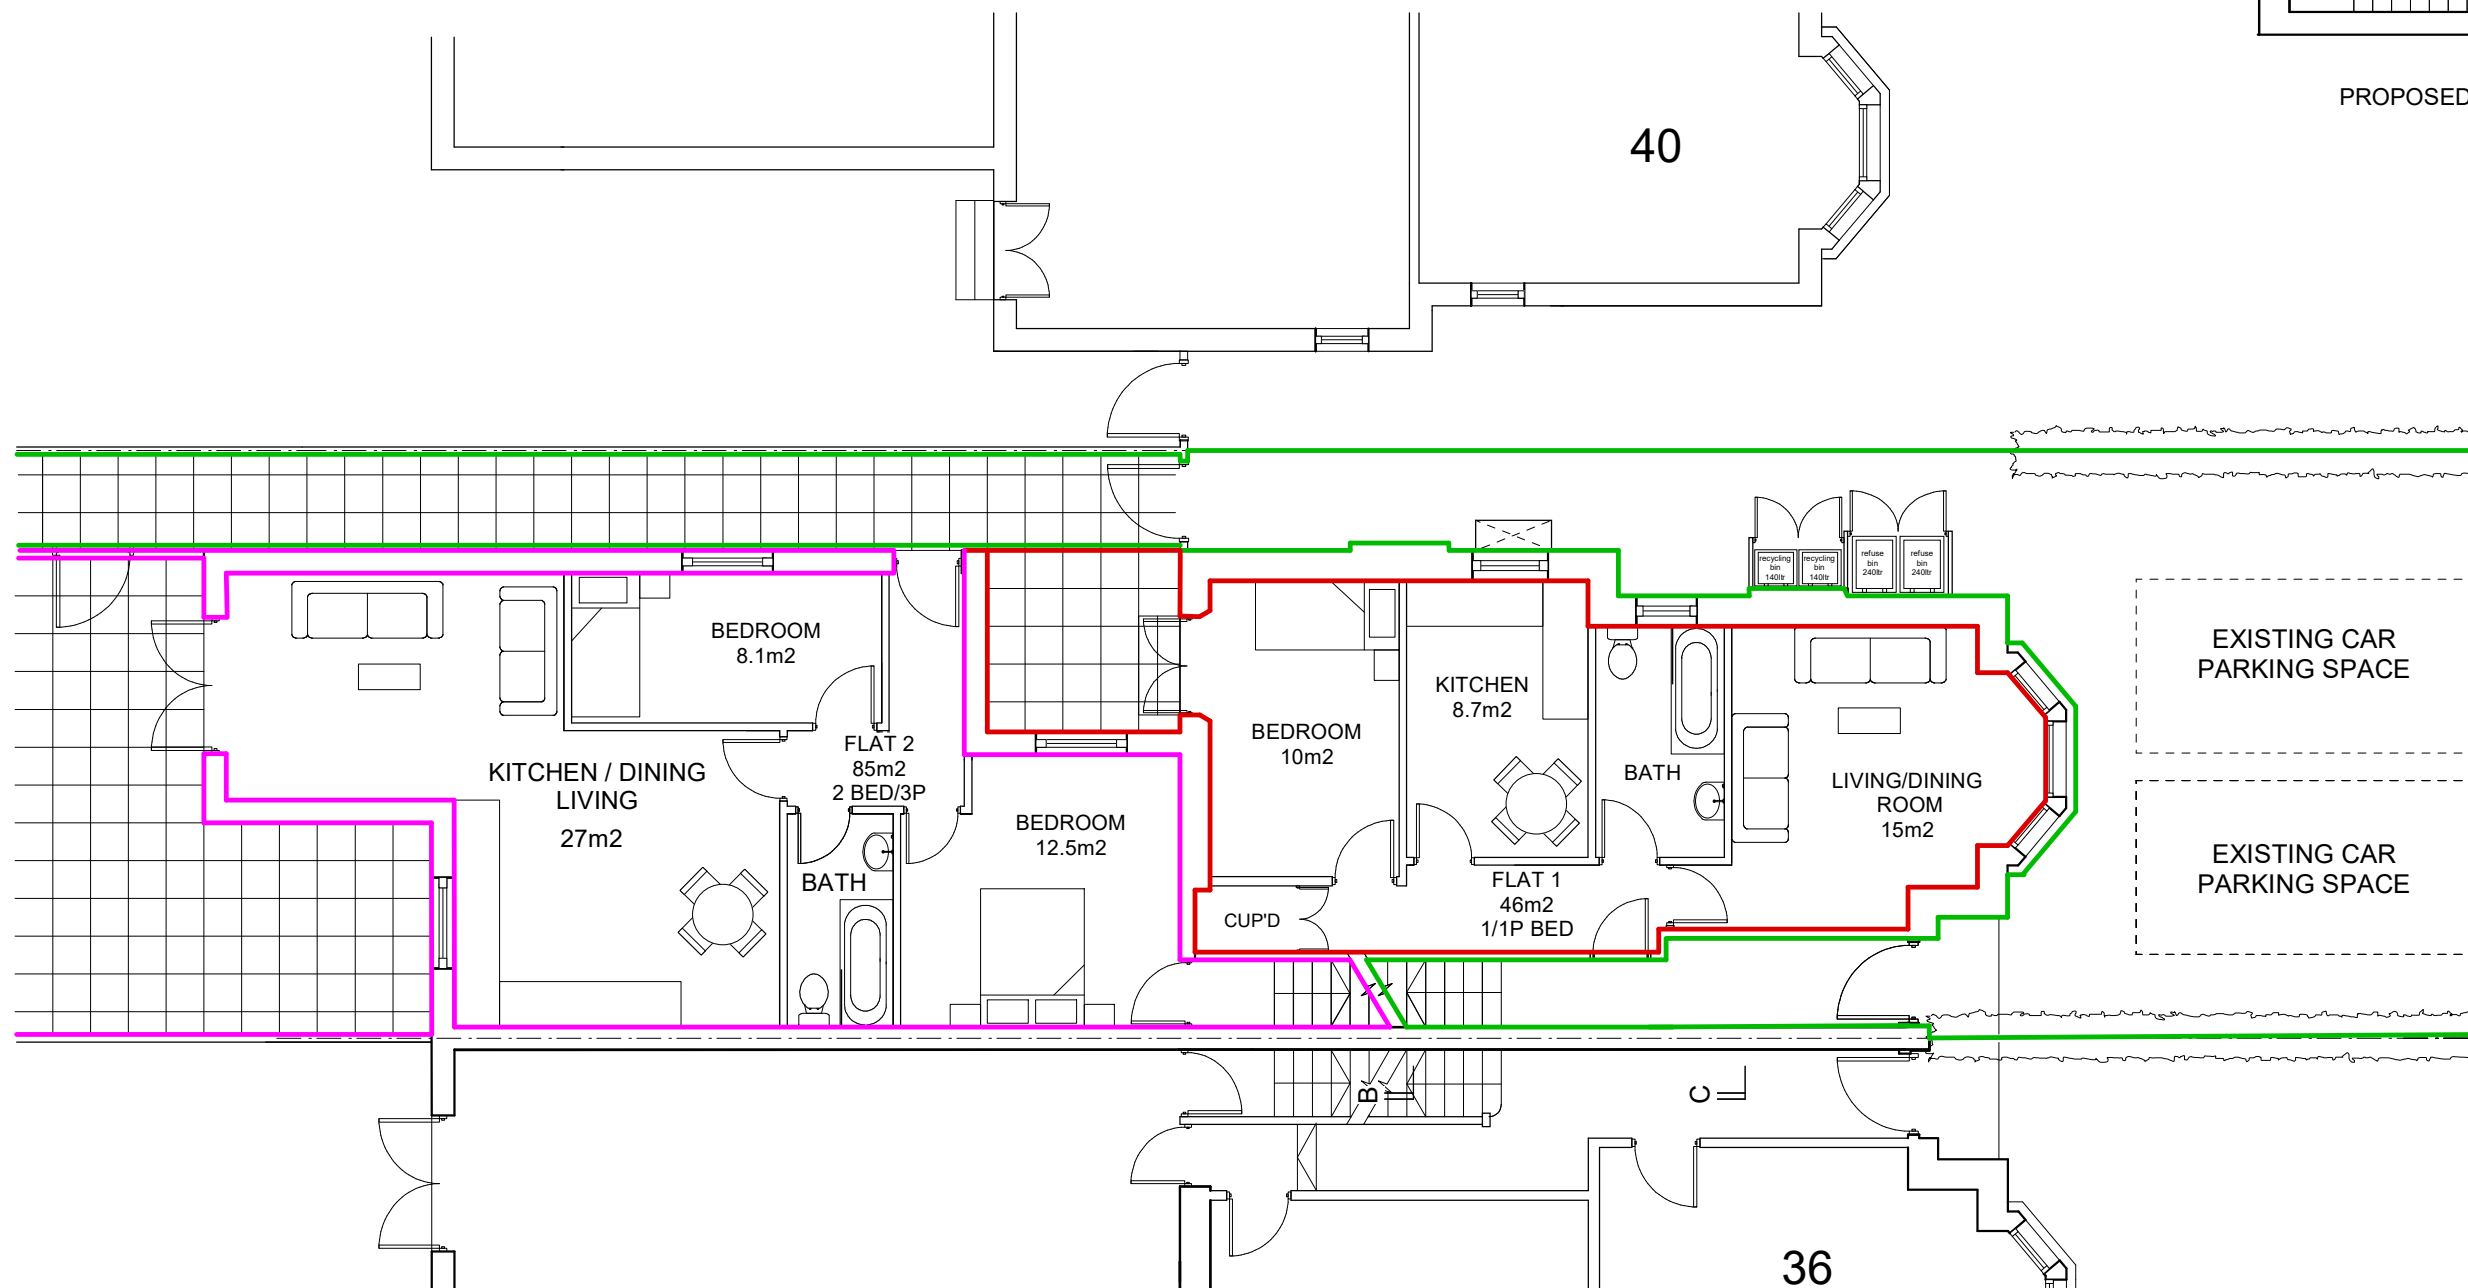


PROPOSED GROUND FLOOR PLAN

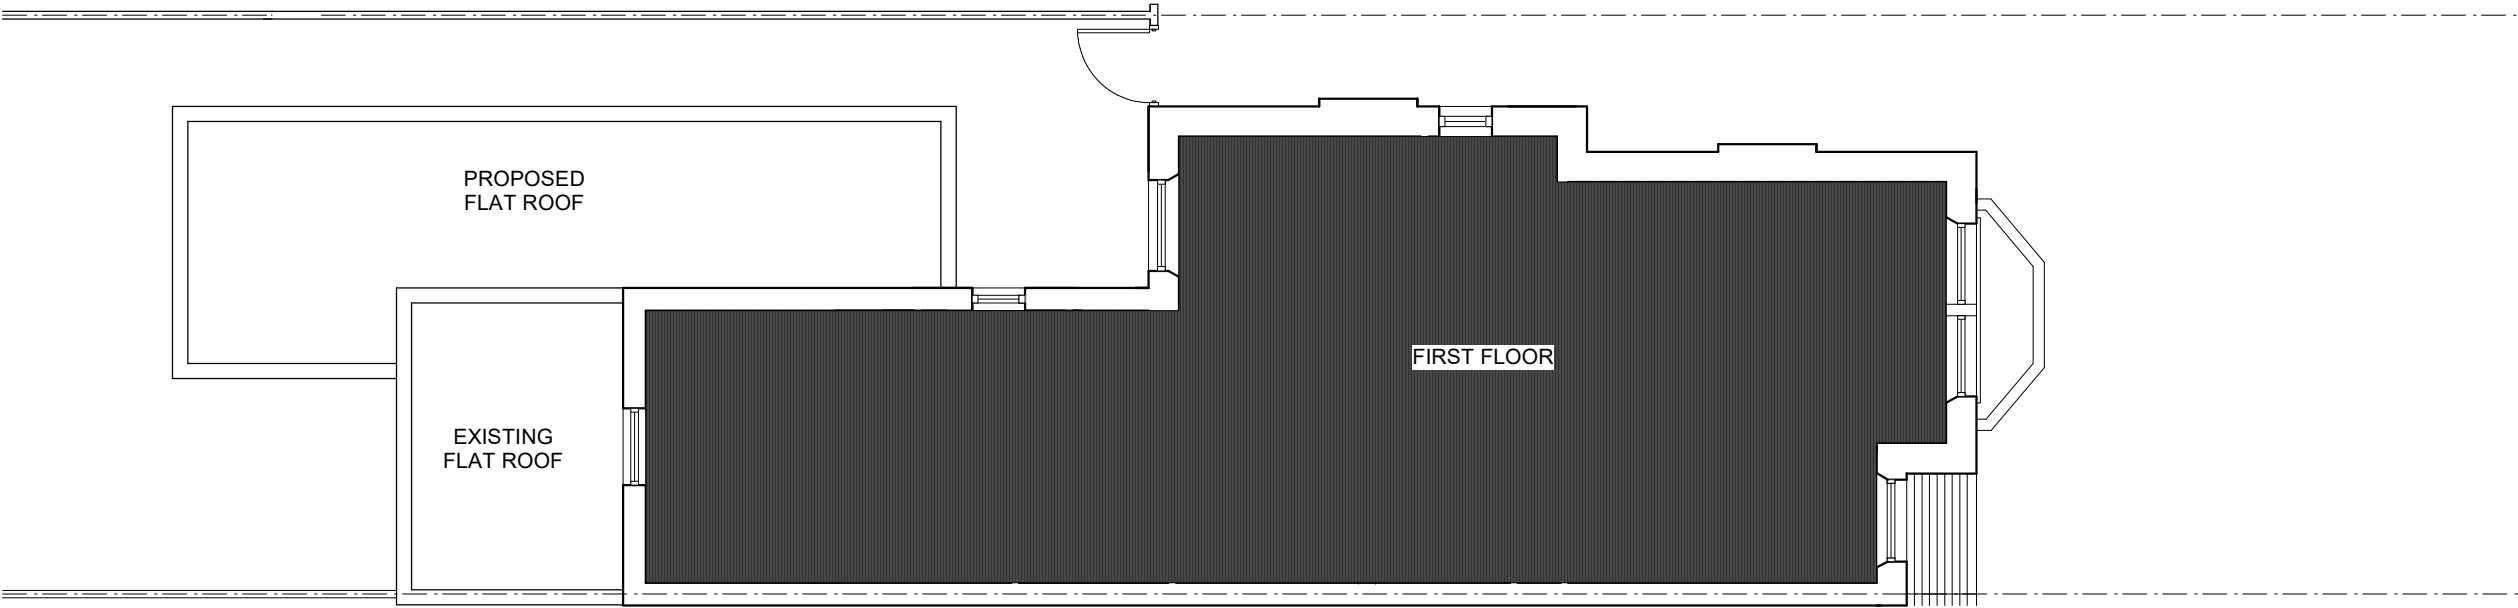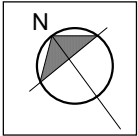

EXISTING ROOF PLAN

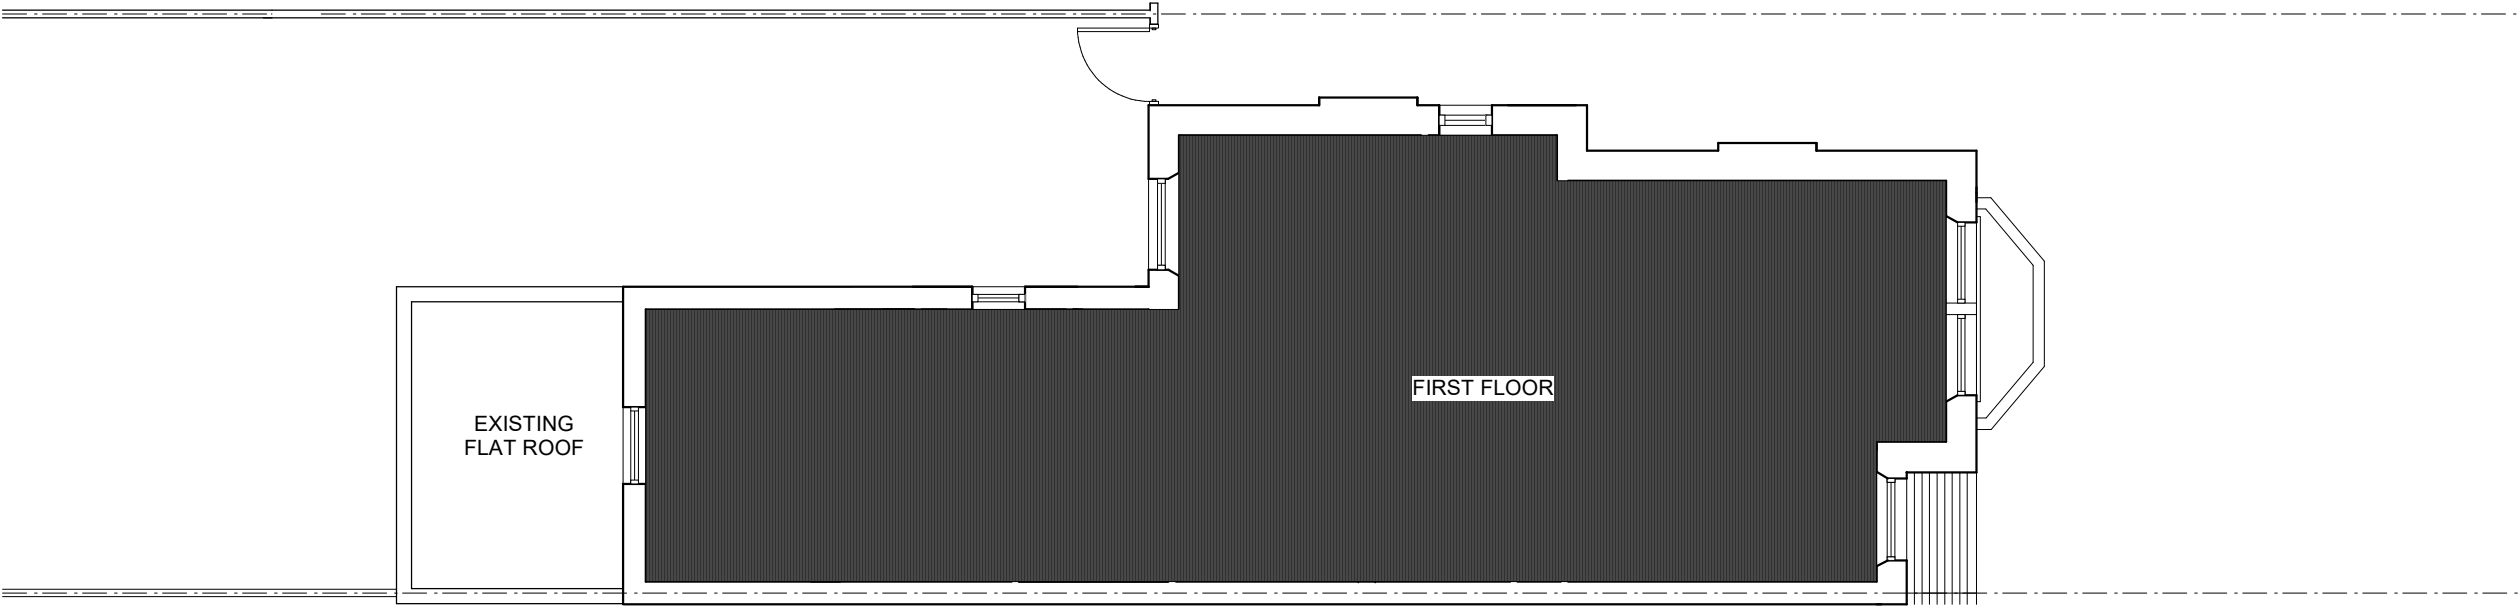


EXISTING ROOF PLAN

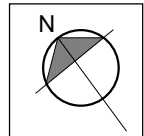

B
A
L
D
R
Y

G
A
R
D
E
N
S

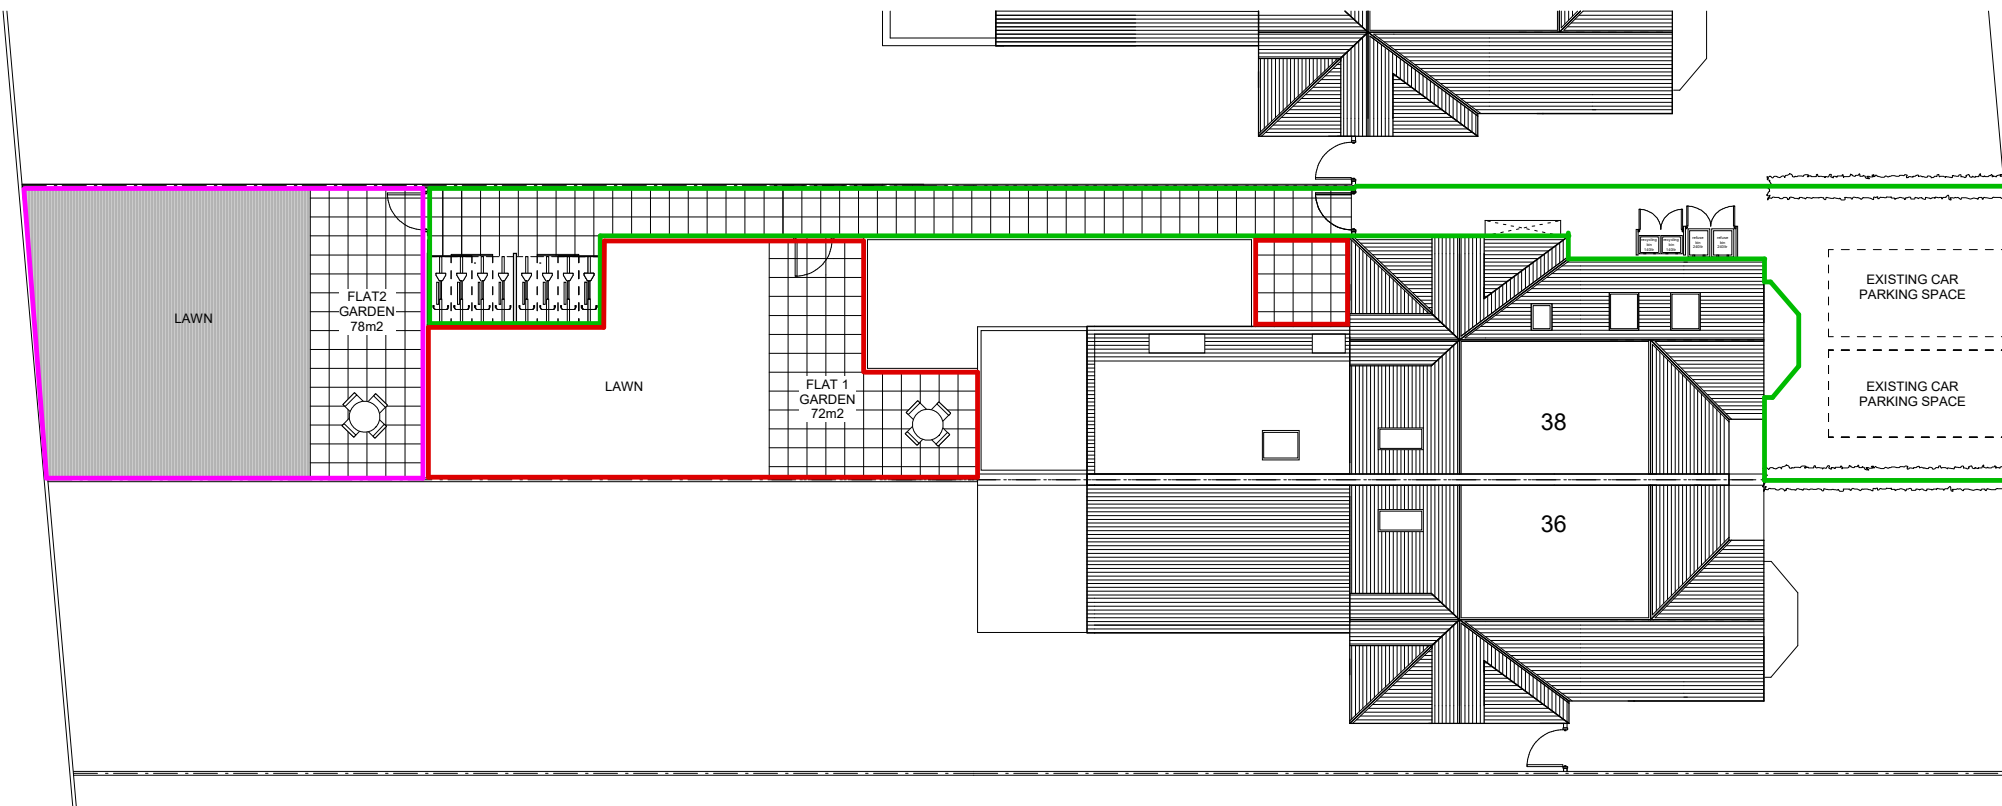


COMMON AREAS		FLAT 1 (1bed /1 p)		FLAT 2 (2 bed / 3p)		KEY
--------------	--	--------------------	--	----------------------	--	-----

PROPOSED SITE PLAN

B
A
L
D
R
Y

G
A
R
D
E
N
S

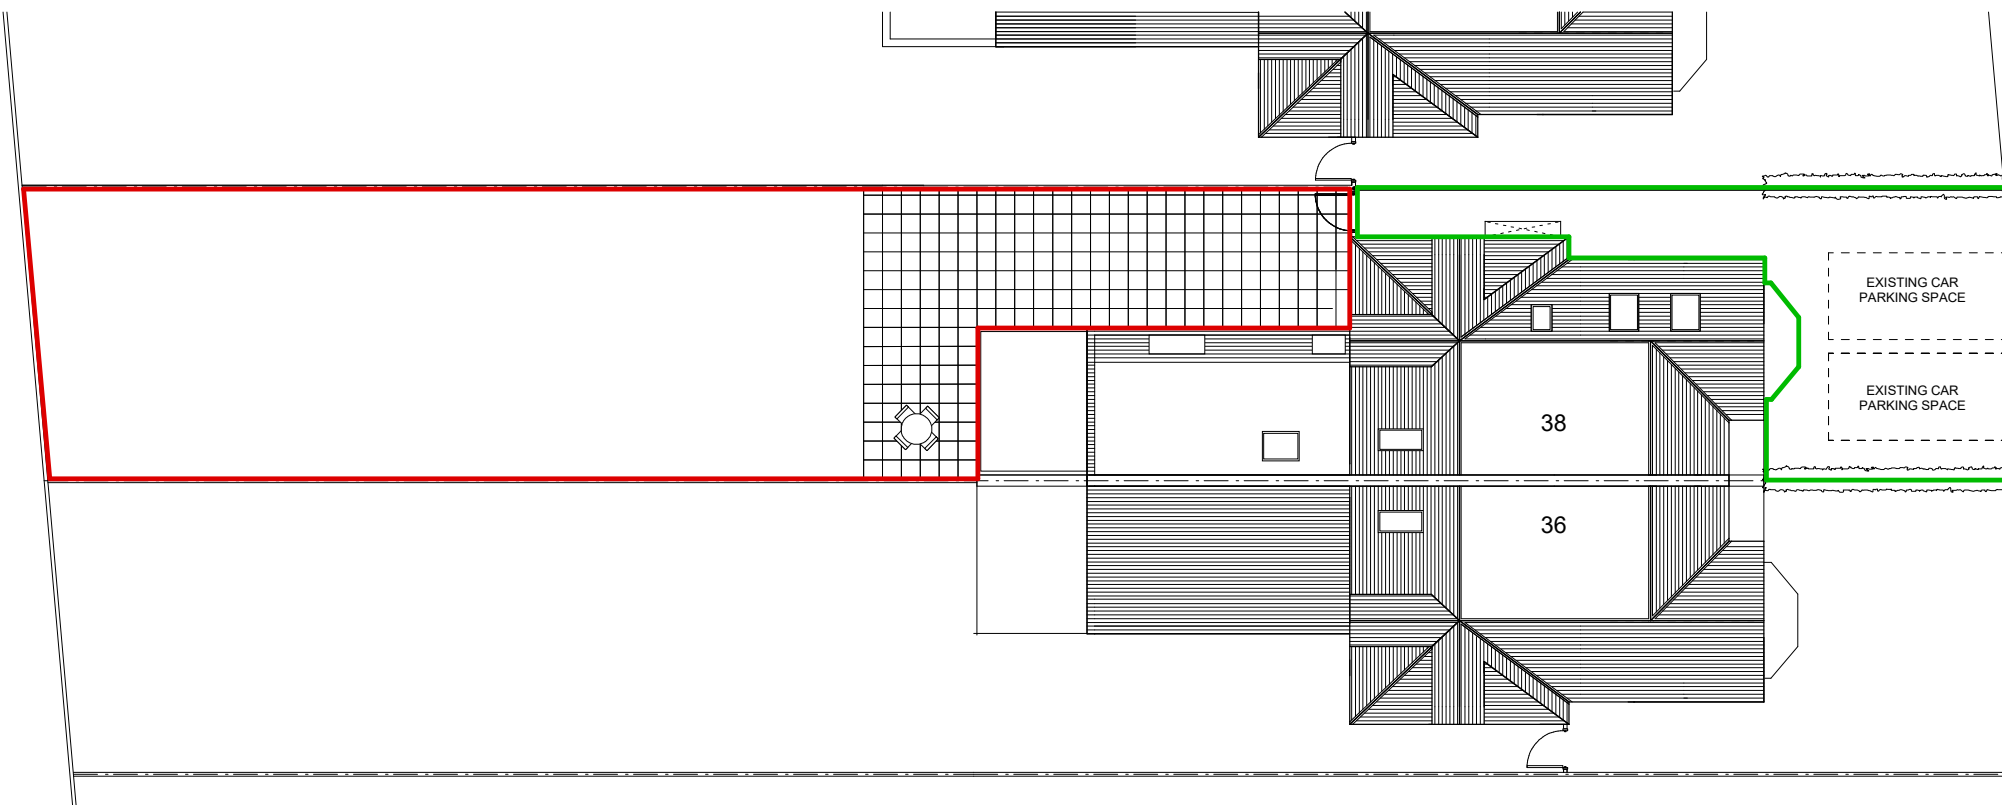

EXISTING SITE PLAN



EXISTING REAR ELEVATION



PROPOSED REAR ELEVATION



PROPOSED SIDE ELEVATION



EXISTING SIDE ELEVATION

RLP

38 Tankerville rd
Streatham Common
SW16 5LP

Contact: Pamela Fitzsimons
Tel/Fax: mob: 07790154232
e-mail: pamela@taltd.info

PROJECT

38 BALDRY GARDENS - FLAT 1
London
SW16

SCALE

1:100 @A3

DATE

JULY 2024

CHECKED BY

PJF

REV

DWG NO

38BG/P/06

TITLE:

EXISTING & PROPOSED SIDE ELEVATION


NOTE: This drawing is for PRELIMINARY purposes only

DO NOT SCALE OFF THIS DRAWING

PLANNING


ROOF PLAN OF CYCLE STORAGE AREA
FOR FLAT 1- 5

EXISTING HEDGE

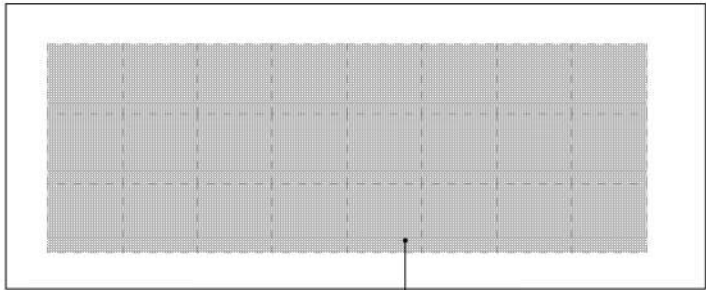


24no 495X460 sedum cassette interlocking trays
to roof of cycle storage

PLAN OF CYCLE STORAGE AREA
FOR FLAT 1 - 5

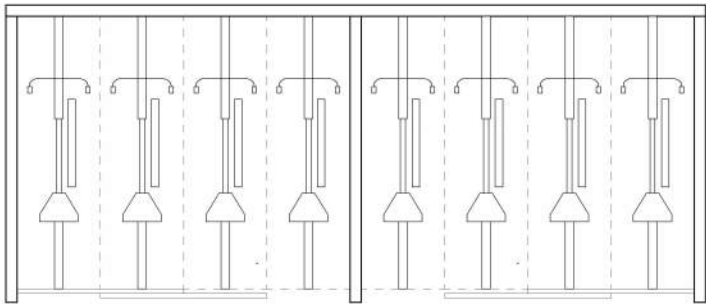

Bespoke Euro cylinder lockable
bike shed for 8no
bike stands for the
residents of Flat 1- 5
constructed in SW TAM timber

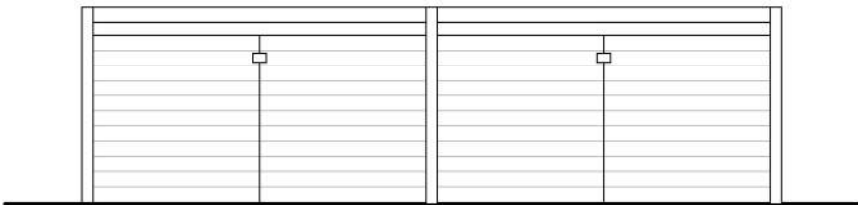


FRONT ELEVATION CYCLE STORAGE AREA
FOR FLAT 1- 5

	FLAT 1 - 1p/1 BED	FLAT 2 - 3p/2 BED	FLAT 3 - 2p/1 BED	FLAT 4 - 2p/1 BED	FLAT 5 - 2p/1 BED	TOTAL
REFUGE	90 litres	90 litres	90 litres	90 litres	90 litres	450 litres
RECYCLING	55 litres	55 litres	55 litres	55 litres	55 litres	275 litres

2no x 240litre refuse bins & 2no 140litre recycling bins




HOUSING UNITS FOR REFUSE & CYCLE STORAGE TO BE
CONSTRUCTED IN SW TAN TIMBER- NATURAL FINISH

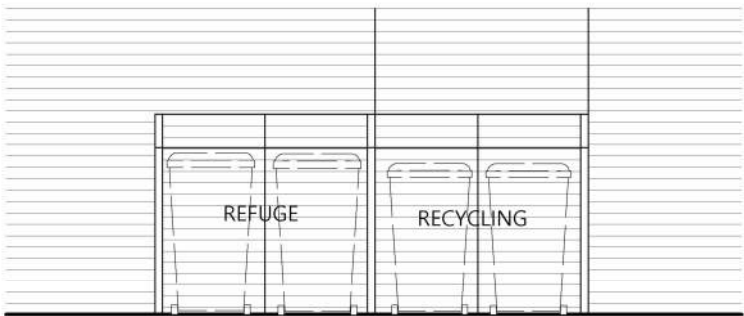


FRONT & SIDE ELEVATIONS OF REFUSE STORAGE FOR ALL FLATS

24no 495X460 sedum
cassette interlocking trays
to roof of cycle
storage

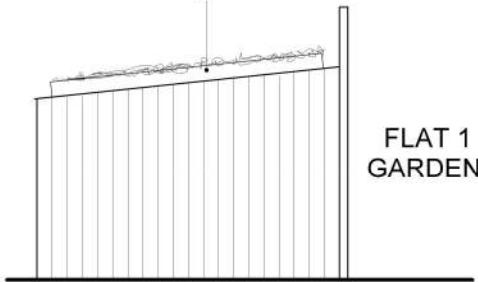

FLAT 1
GARDEN

SIDE ELEVATIONS OF
CYCLE STORAGE FOR ALL FLATS

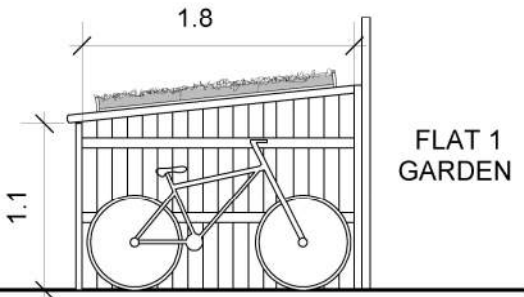

FLAT 1
GARDEN

SECTION OF CYCLE
STORAGE AREA
FOR FLAT 1,2&3