


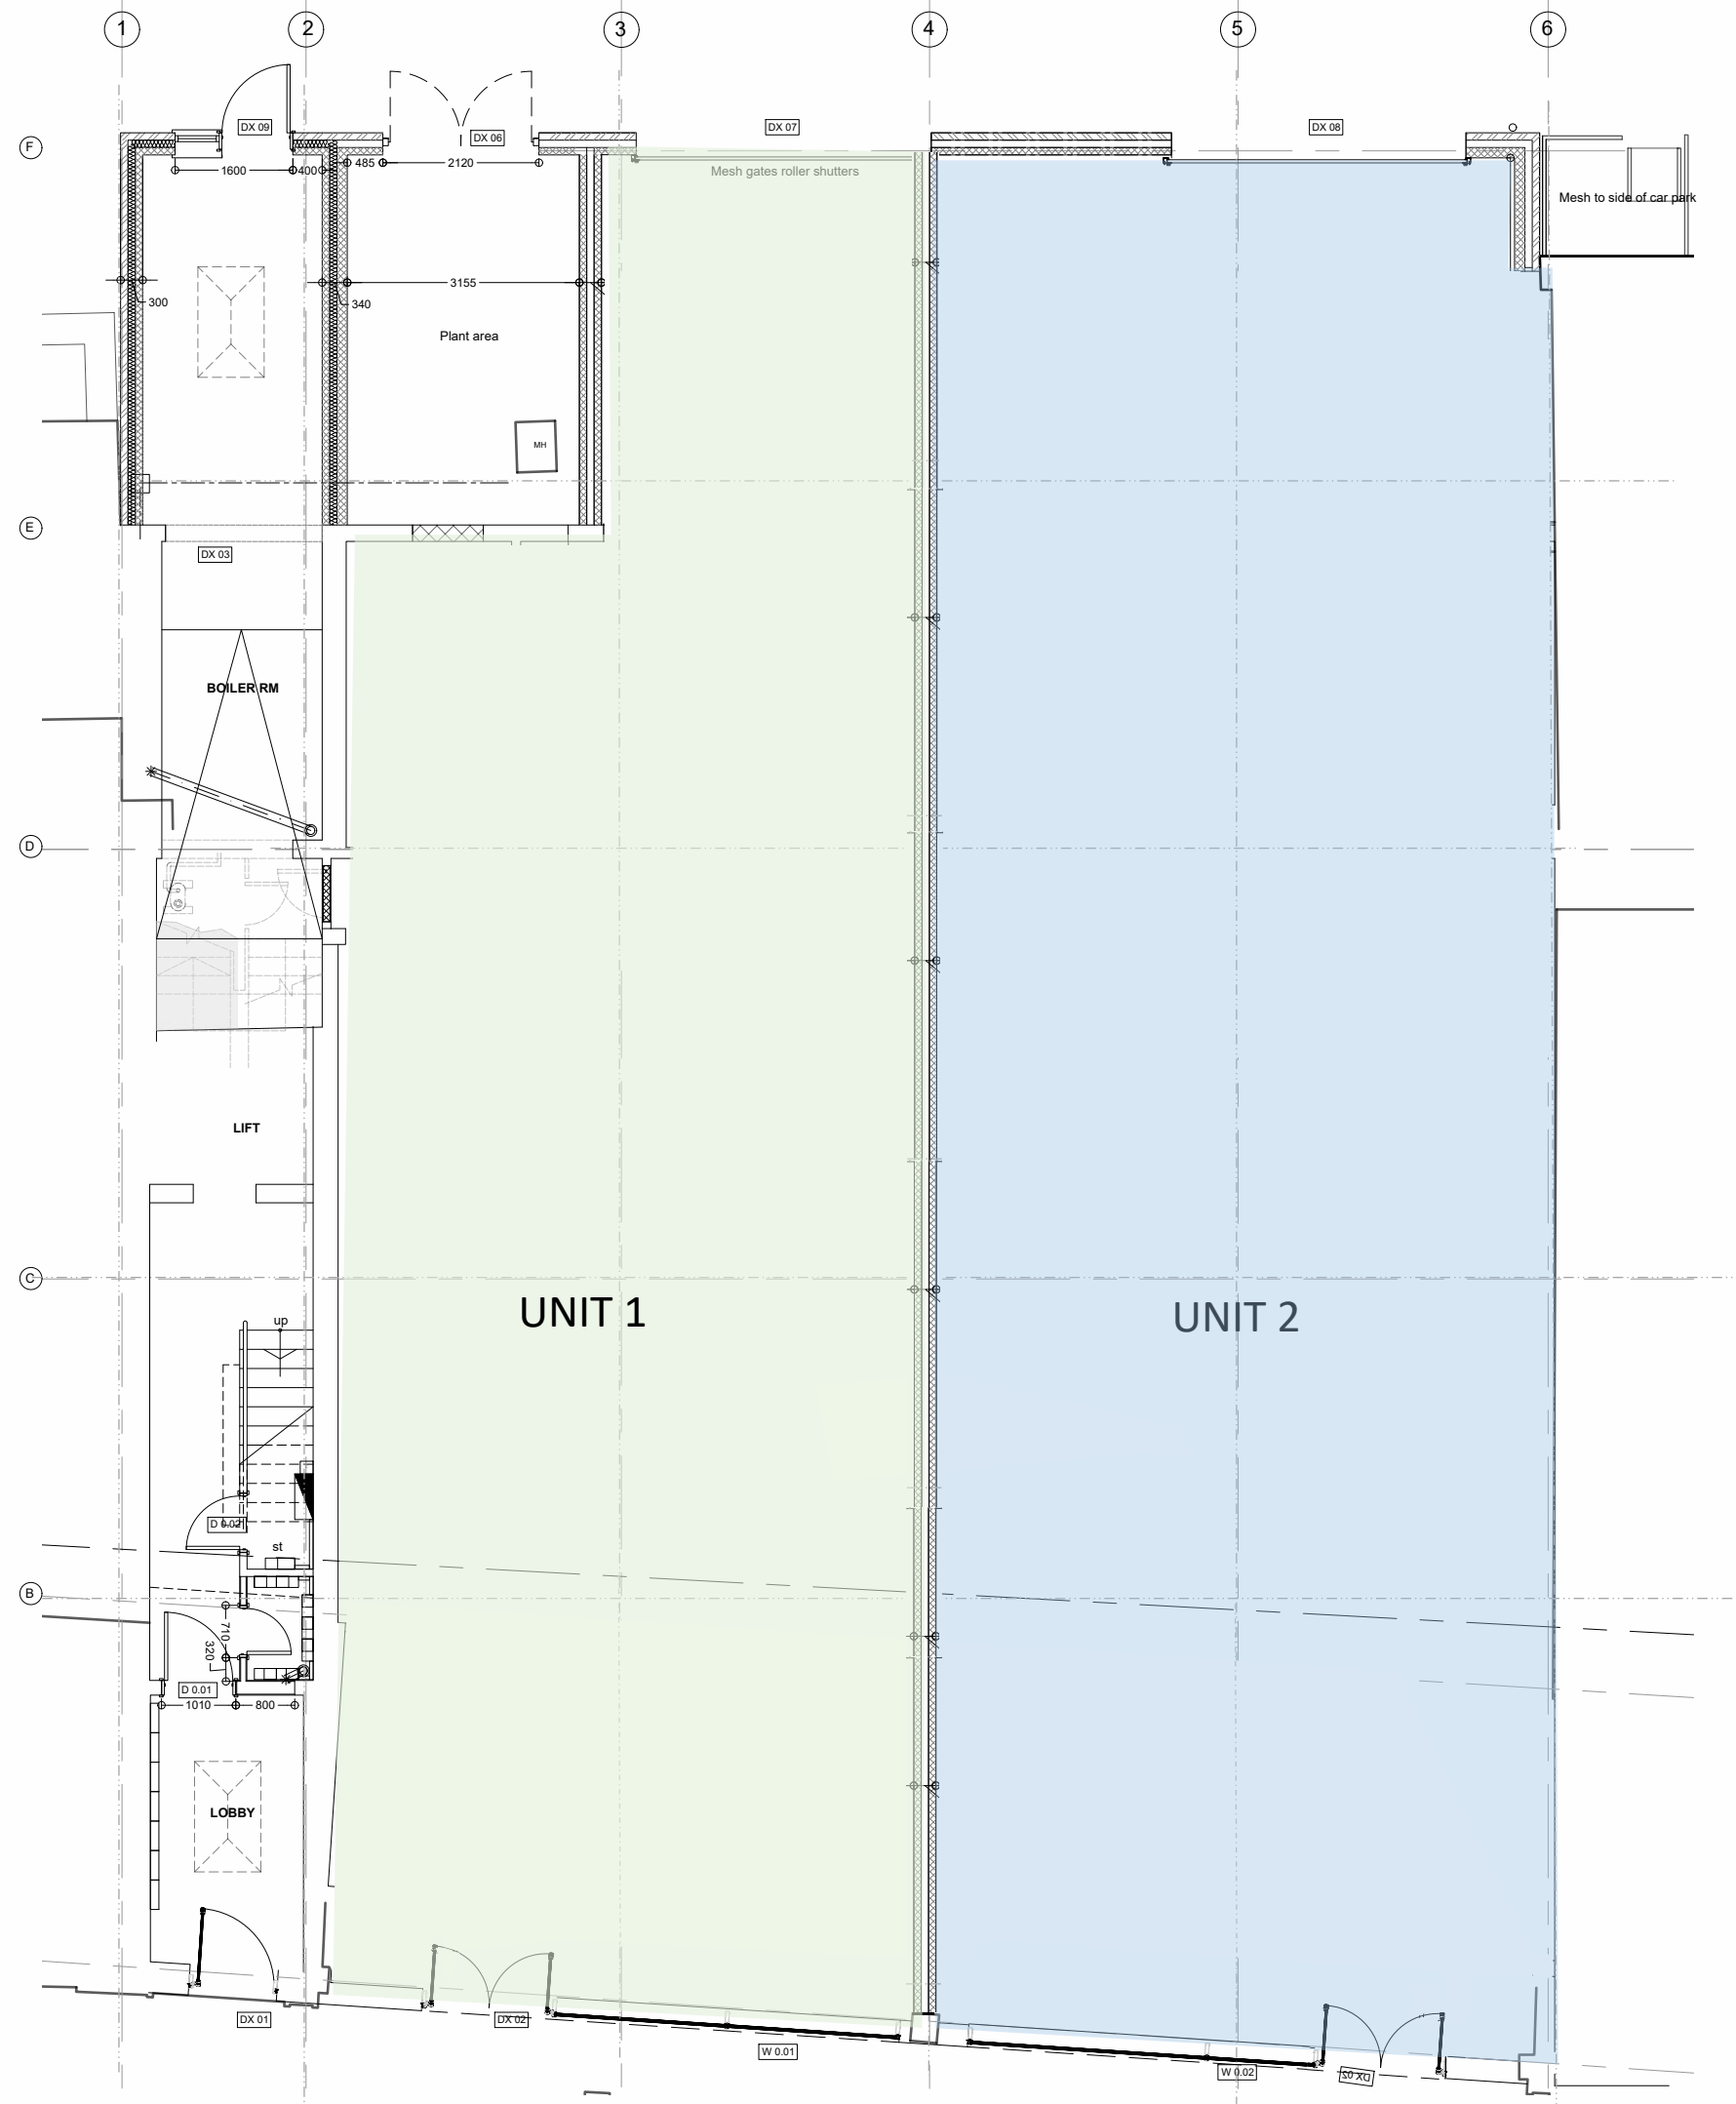

SETTING OUT PLAN - GROUND FLOOR
Scale 1:50 @ A1

client	161 CHS Ltd		
project	161 Clapham High Street Clapham London SW4 7ST		
drawing	Setting Out- Ground Floor		
date	AUG-24	drawn	BN
		checked	
scale	1:50 @ A1	drawer no	dwg no 3381-124E



client	161 CHS Ltd		
project	161 Clapham High Street Clapham London SW4 7ST		
drawing	Proposed - Front Elevation		
date	AUG-24	drawn	BN
		checked	DR
scale	1:50 @ A1	drawer	no
		dwg	no3381-111B