
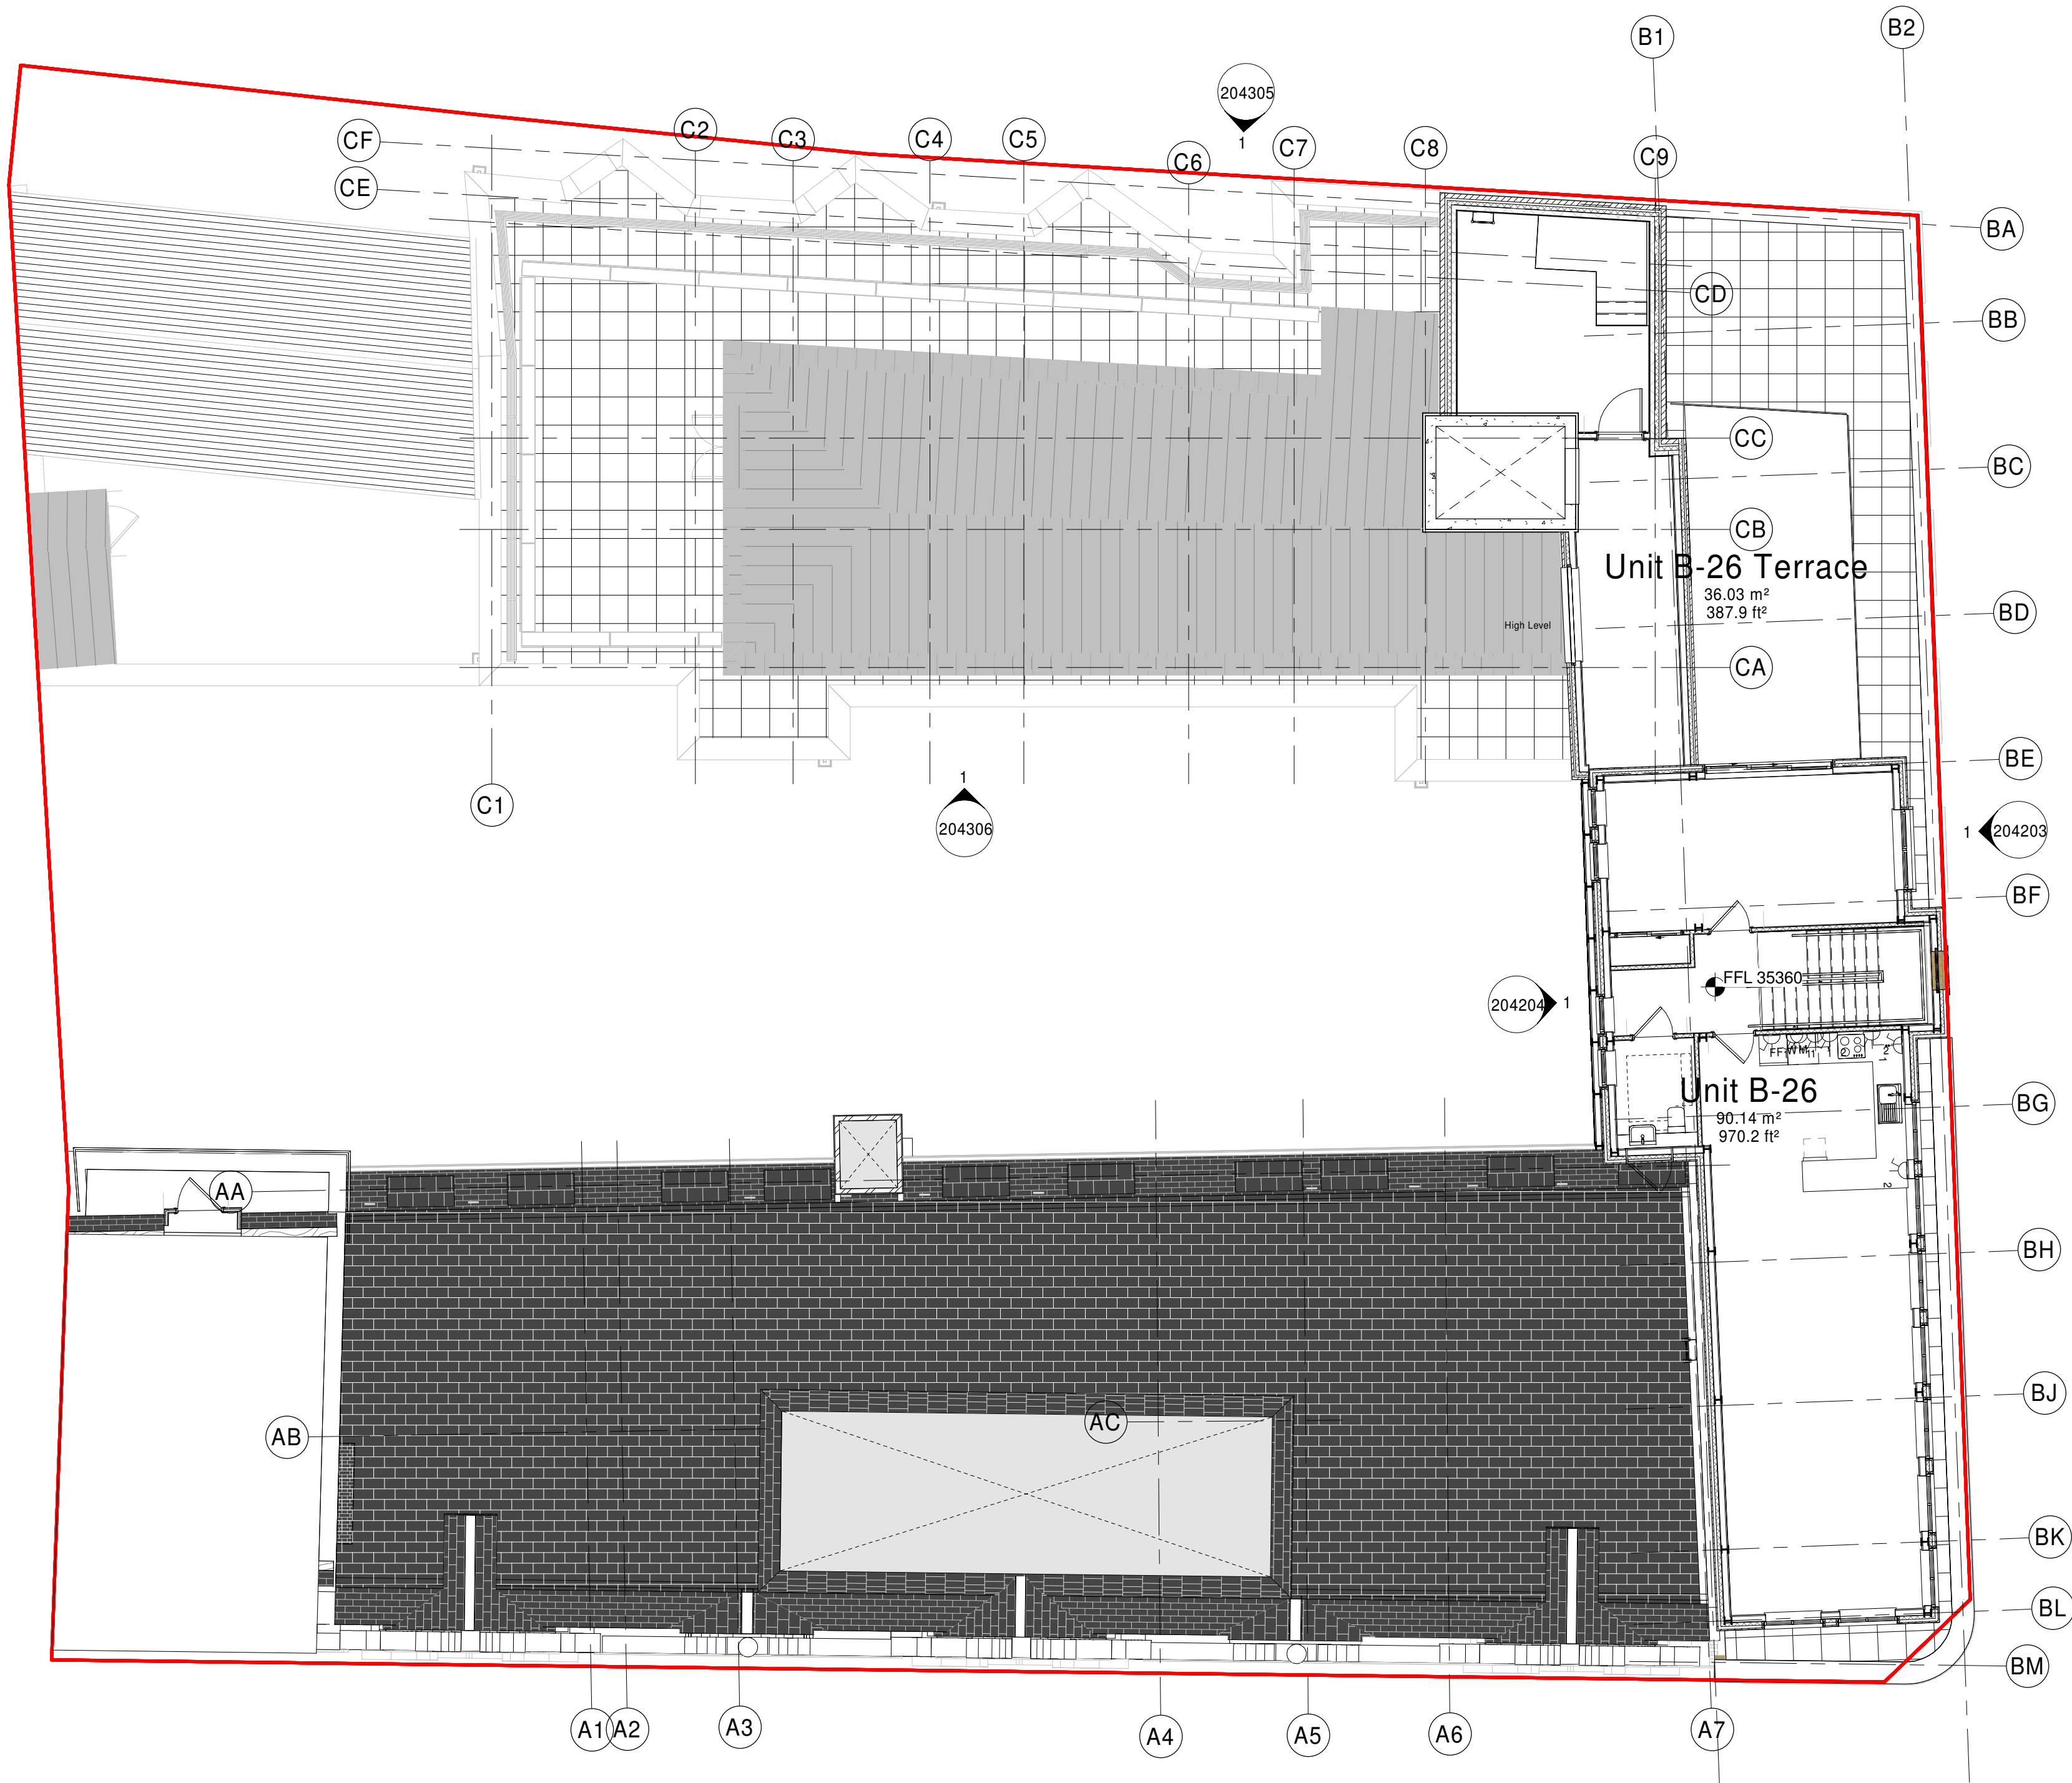


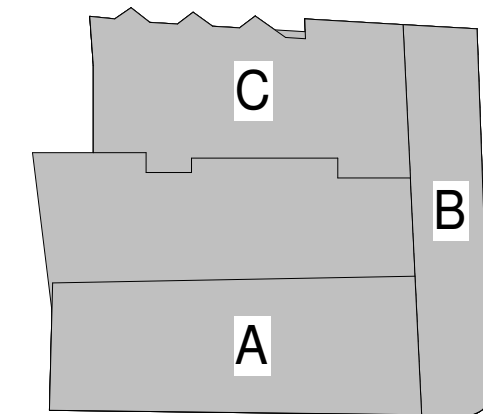

Level 4-All Blocks-GA Planning
1 : 100

Room Schedule-Ground Floor-Net Area			
Number	Name	Area	Comments
GF-01	Entrance Lobby	12.6 m²	Ground Floor
GF-02	Staircase-Lift Lobby	13.7 m²	Ground Floor
GF-03	Passage-01	4.8 m²	Ground Floor
GF-04	Bins-Com.	22.0 m²	Ground Floor
GF-05	Retail No156-158	208.5 m²	Ground Floor
GF-06	Passage-02	12.0 m²	Ground Floor
GF-07	156-158 Storage 01	11.0 m²	Ground Floor
GF-08	156-158 Storage 02	3.0 m²	Ground Floor
GF-09	Passage-03	8.4 m²	Ground Floor
GF-10	Bina-Ret.	15.3 m²	Ground Floor
GF-11	Retail No160	90.7 m²	Ground Floor
GF-12	Passage-04	18.0 m²	Ground Floor
GF-13	160 Storage 01	26.8 m²	Ground Floor
GF-15	160 Storage 02	1.0 m²	Ground Floor
GF-16	Retail No162	108.7 m²	Ground Floor
GF-17	Mez. Stair 162-164	11.9 m²	Ground Floor
GF-18	Passage-05	9.1 m²	Ground Floor
GF-19	162 Storage	28.3 m²	Ground Floor
GF-20	Retail No164	136.7 m²	Ground Floor
GF-21	Passage-06	7.7 m²	Ground Floor
Grand total: 20		750.2 m²	

NORTH SIGN:

SCALE BAR:

GRID REFERENCE:

GRID SETTING OUT:

PLOT CODES:

Unit A-01
50.00 m²
538.2 ft²

Block - Flat number
GIA in sqm
GIA in feet

FLOOR FINISH LEVEL:

FFL indicates the finish floor level with the new build-up