





Site Plan


1 : 1250

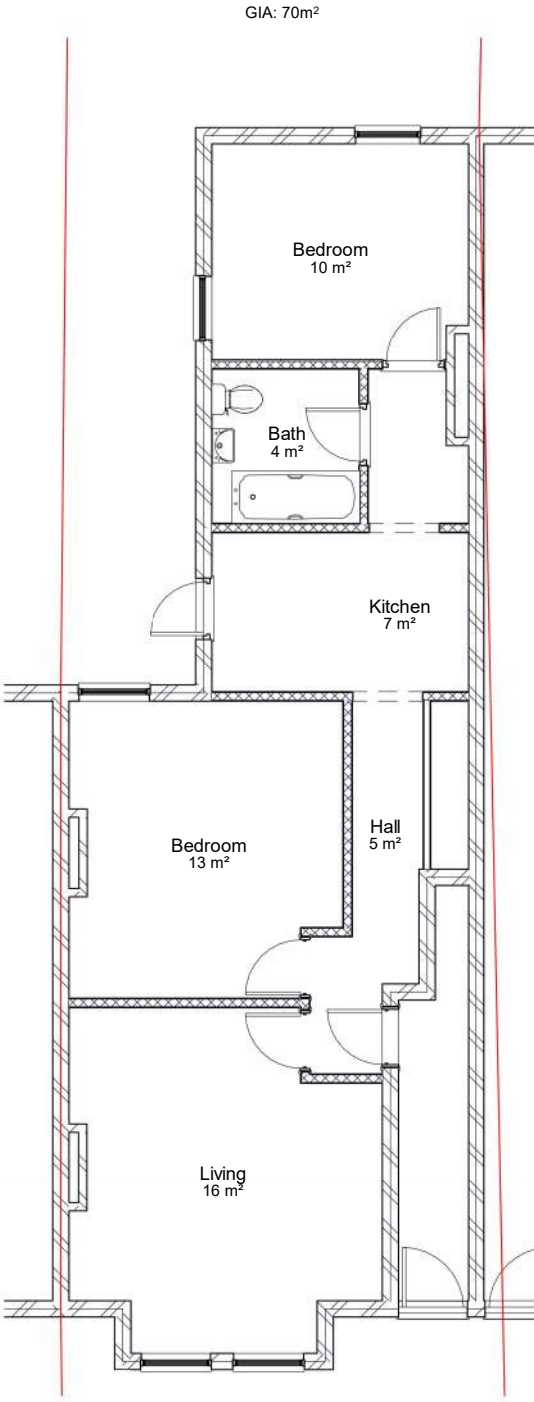

GFL
1 : 100

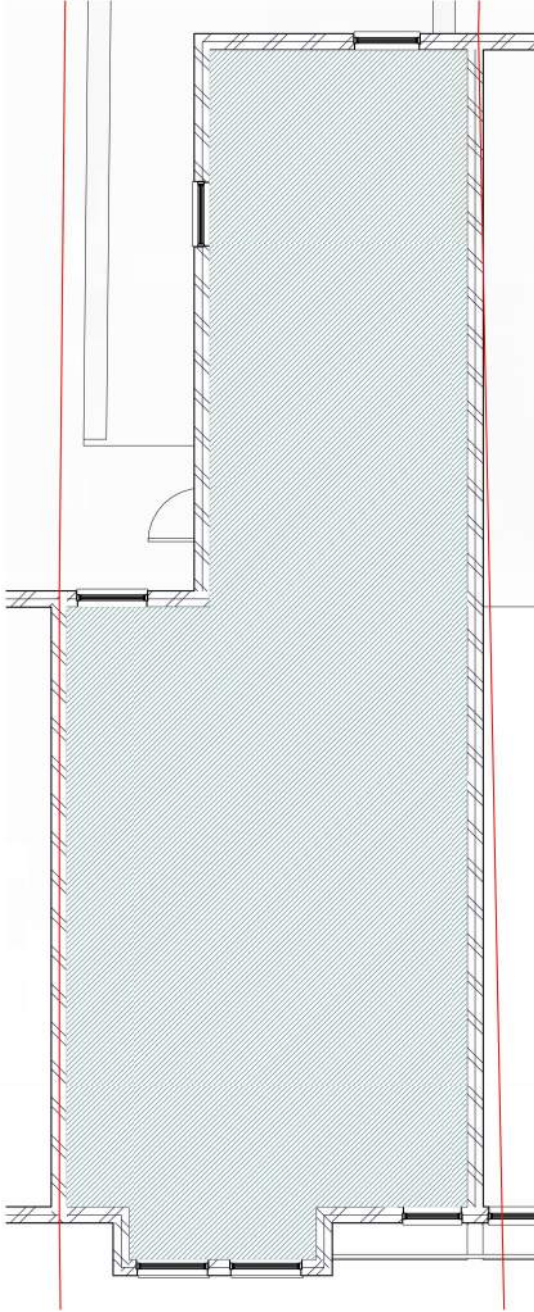

FFL
1 : 100

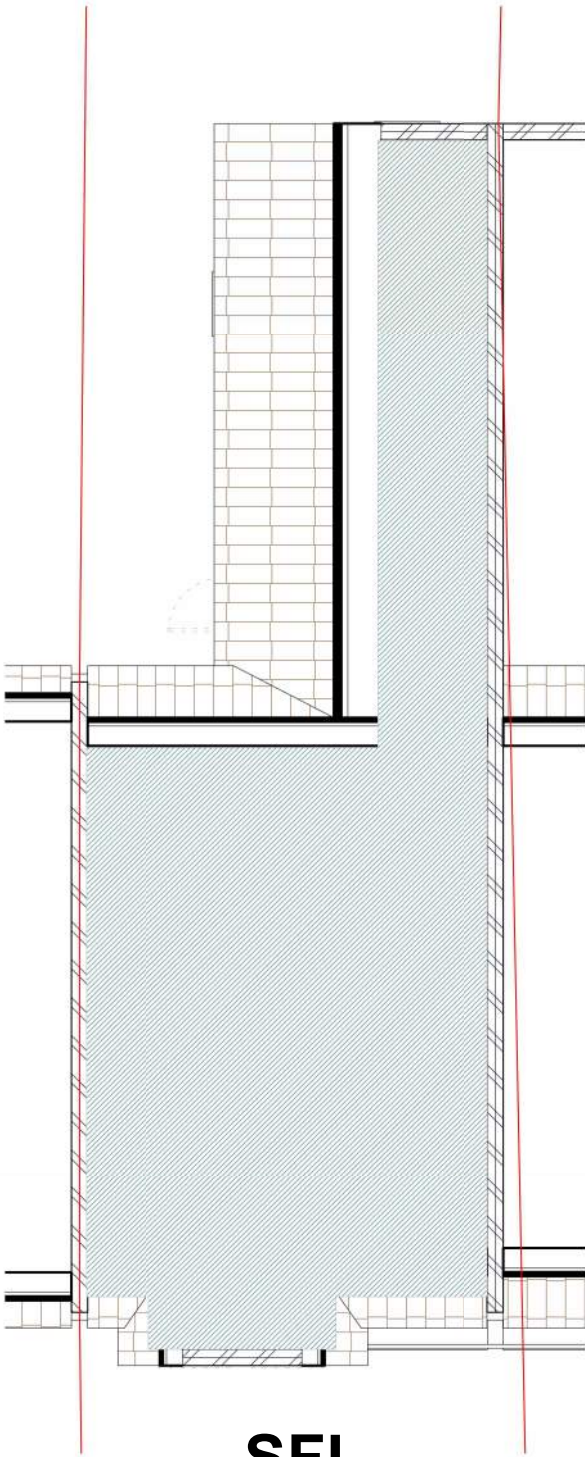

SFL
1 : 100

NOTES:

TITLE:
Site & Existing Plans

SITE:
Alex Keating
107a Cavendish Road,
London,
SW12 0BN

PROJECT NO.
2024_11_SW12_KEA


SCALE AT A3 DRAWING NO.
As indicated
DRAWN BY
A100
CHECKED BY

DATE.
17/12/2024

REVISION.


THE COPYRIGHT of this drawing is vested in Brunthan Yoheswaran and it may not be reproduced in whole or in part or used for the manufacture of any article without the express permission of the copyright holder.
THE SPECIFICATION in this drawing to be read in accordance with all relevant plans, elevations, sections and structural engineer's designs/calculations
ALL DIMENSIONS to be confirmed on site before the manufacture of any article
DO NOT SCALE off Drawing except for approximate dimensions
ALL WORKMANSHIP to be undertaken in strict accordance with the approval of the LPA Building Control Officer and in strict adherence with current British Standards and codes of practice
ALL MATERIALS used in construction or manufacture to be in strict adherence with current British Standards and codes of practice
ALL NEW GLAZING AND WINDOWS to meet thermal and ventilation requirements of current LPA Building Regulations
ELECTRICAL EQUIPMENT/WIRING: design & installation of all electrical wiring & related fittings to be carried out by an appd. electrical engineer in strict adherence to current British Standards and codes of practice
GAS/PLUMBING APPLIANCES: design & installation of all gas & plumbing & related fittings, appliances and equipment to be carried out by an appd. gas engineer in strict adherence to current British Standards and codes of practice

No	R.Desc	R.Date
----	--------	--------

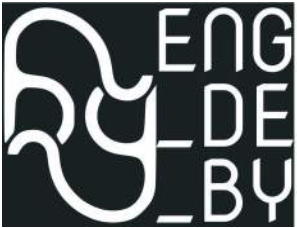


Planning &
Structural Engineering

info@engdeby.co.uk
+44 (0)7886 701 813

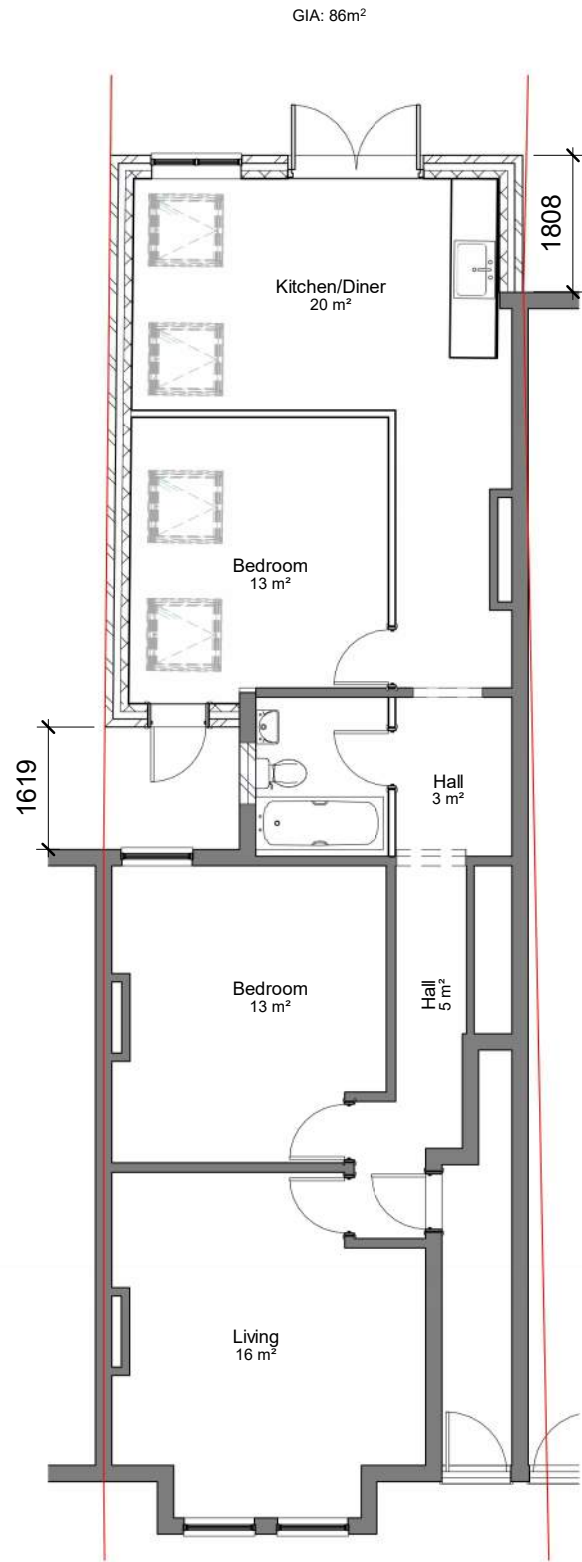

Proposed GFL
1 : 100

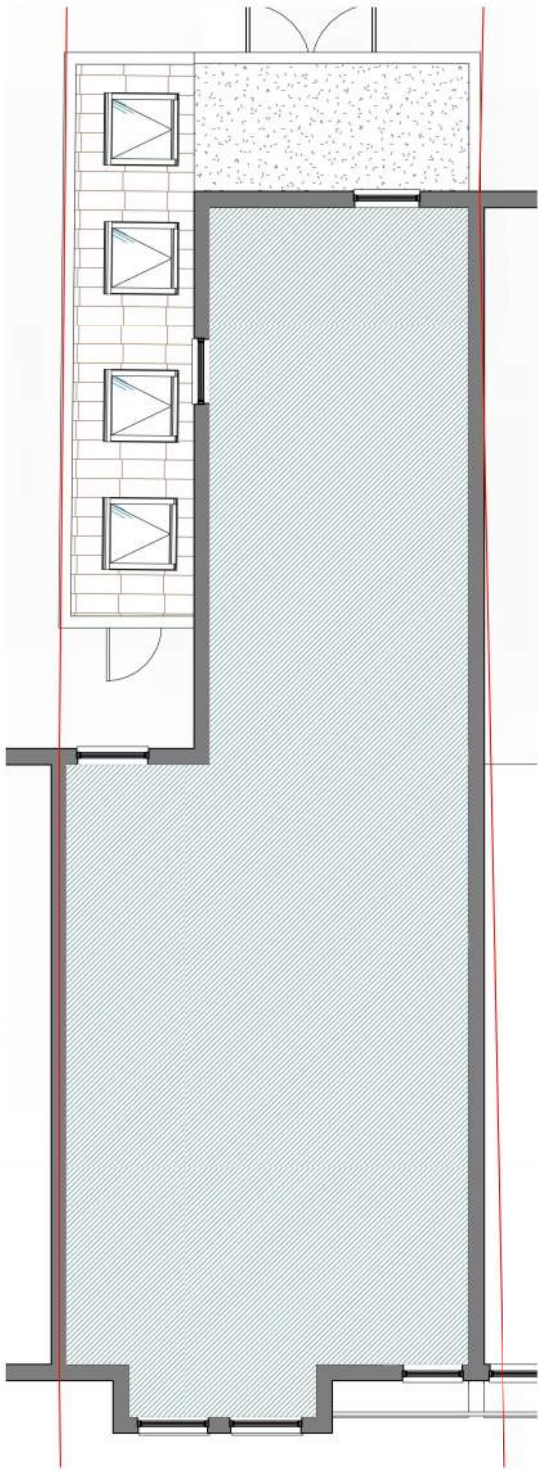


Proposed FFL
1 : 100

- PRECEDENTS**
- 23/02825/FUL - Side infill extension with pitched roof
 - 23/01336/FUL - Side infill extension with pitched roof
 - 19/03415/FUL - side infill extension with pitched roof
 - 23/00677/FUL - side infill & rear extension extending beyond existing rear elevation

NOTES:

TITLE:
Proposed Plans

SITE:
Alex Keating
107a Cavendish Road,
London,
SW12 0BN

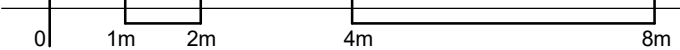

PROJECT NO.
2024_11_SW12_KEA

SCALE AT A3 DRAWING NO.
1 : 100 A101

DRAWN BY
BY

CHECKED BY
BY

DATE
17/12/2024

REVISION

THE COPYRIGHT of this drawing is vested in Brunthan Yoheswaran and it may not be reproduced in whole or in part or used for the manufacture of any article without the express permission of the copyright holder

THE SPECIFICATION in this drawing to be read in accordance with all relevant plans, elevations, sections and structural engineer's designs/calculations

ALL DIMENSIONS to be confirmed on site before the manufacture of any article

DO NOT SCALE off Drawing except for approximate dimensions

ALL WORKMANSHIP to be undertaken in strict accordance with the approval of the LPA Building Control Officer and in strict adherence with current British Standards and codes of practice


ALL MATERIALS used in construction or manufacture to be in strict adherence with current British Standards and codes of practice

ALL NEW GLAZING AND WINDOWS to meet thermal and ventilation requirements of current LPA Building Regulations

ELECTRICAL EQUIPMENT/WIRING: design & installation of all electrical wiring & related fittings to be carried out by an appd. electrical engineer in strict adherence to current British Standards and codes of practice

GAS/PLUMBING APPLIANCES: design & installation of all gas & plumbing & related fittings, appliances and equipment to be carried out by an appd. gas engineer in strict adherence to current British Standards and codes of practice

No	R.Desc	R.Date
----	--------	--------

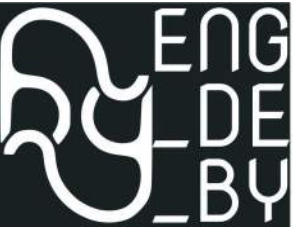


Planning &
Structural Engineering


info@engdeby.co.uk
+44 (0)7886 701 813




FRONT
1 : 100

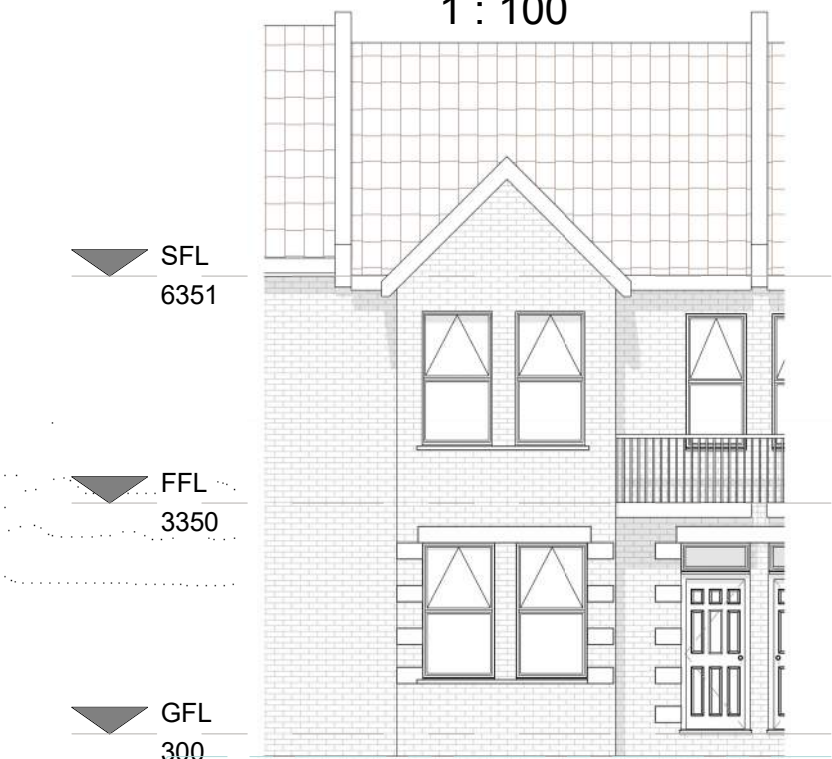

Proposed Front
1 : 100

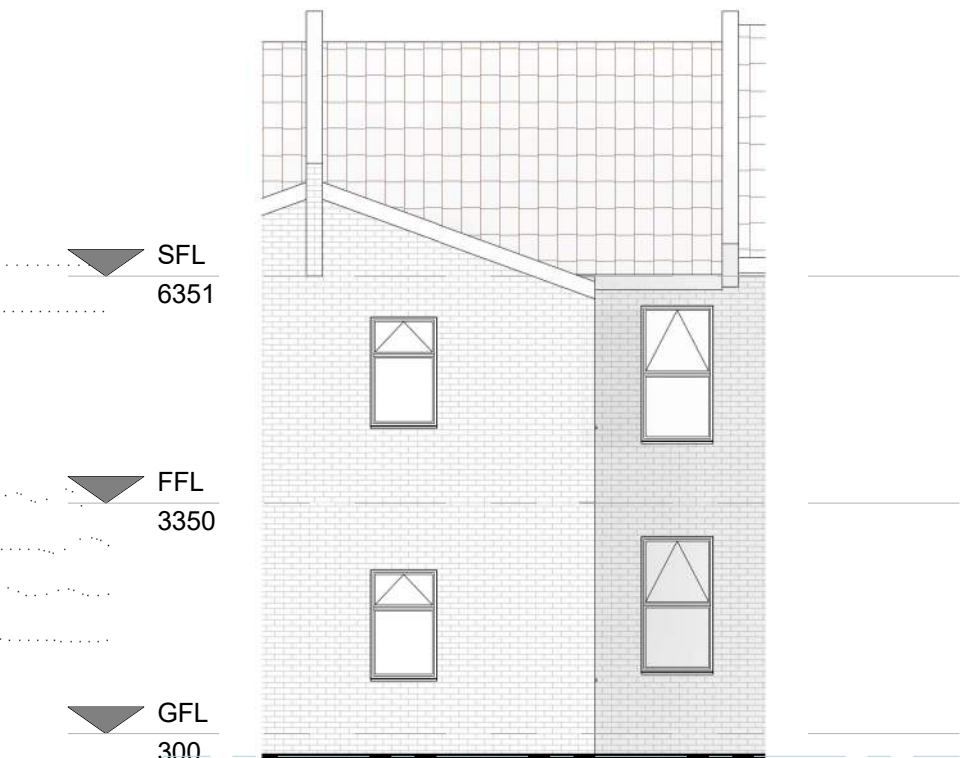

REAR
1 : 100

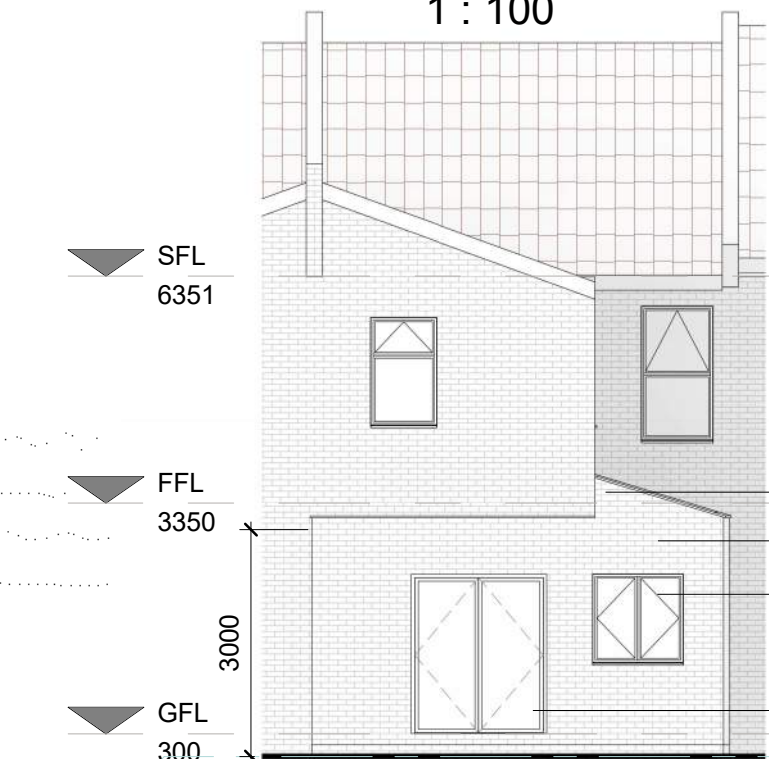

Proposed Rear
1 : 100

NOTES:

TITLE: Extng & Proposed Elevations
SITE: Alex Keating
107a Cavendish Road,
London,
SW12 0BN




PROJECT NO. 2024_11_SW12_KEA
SCALE AT A3 DRAWING NO. 1 : 100 A102
DATE. 17/12/2024

DRAWN. BY
CHECKED. BY
REVISION.


THE COPYRIGHT of this drawing is vested in Brunthan Yoheswaran and it may not be reproduced in whole or in part or used for the manufacture of any article without the express permission of the copyright holder.
THE SPECIFICATION in this drawing to be read in accordance with all relevant plans, elevations, sections and structural engineer's designs/calculations
ALL DIMENSIONS to be confirmed on site before the manufacture of any article
DO NOT SCALE off Drawing except for approximate dimensions
ALL WORKMANSHIP to be undertaken in strict accordance with the approval of the LPA Building Control Officer and in strict adherence with current British Standards and codes of practice
ALL MATERIALS used in construction or manufacture to be in strict adherence with current British Standards and codes of practice
ALL NEW GLAZING AND WINDOWS to meet thermal and ventilation requirements of current LPA Building Regulations
ELECTRICAL EQUIPMENT/WIRING: design & installation of all electrical wiring & related fittings to be carried out by an appd. electrical engineer in strict adherence to current British Standards and codes of practice
GAS/PLUMBING APPLIANCES: design & installation of all gas & plumbing & related fittings, appliances and equipment to be carried out by an appd. gas engineer in strict adherence to current British Standards and codes of practice

No	R.Desc	R.Date
----	--------	--------

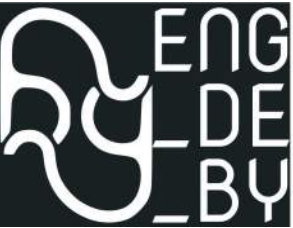

Planning &
Structural Engineering

info@engdeby.co.uk
+44 (0)7886 701 813

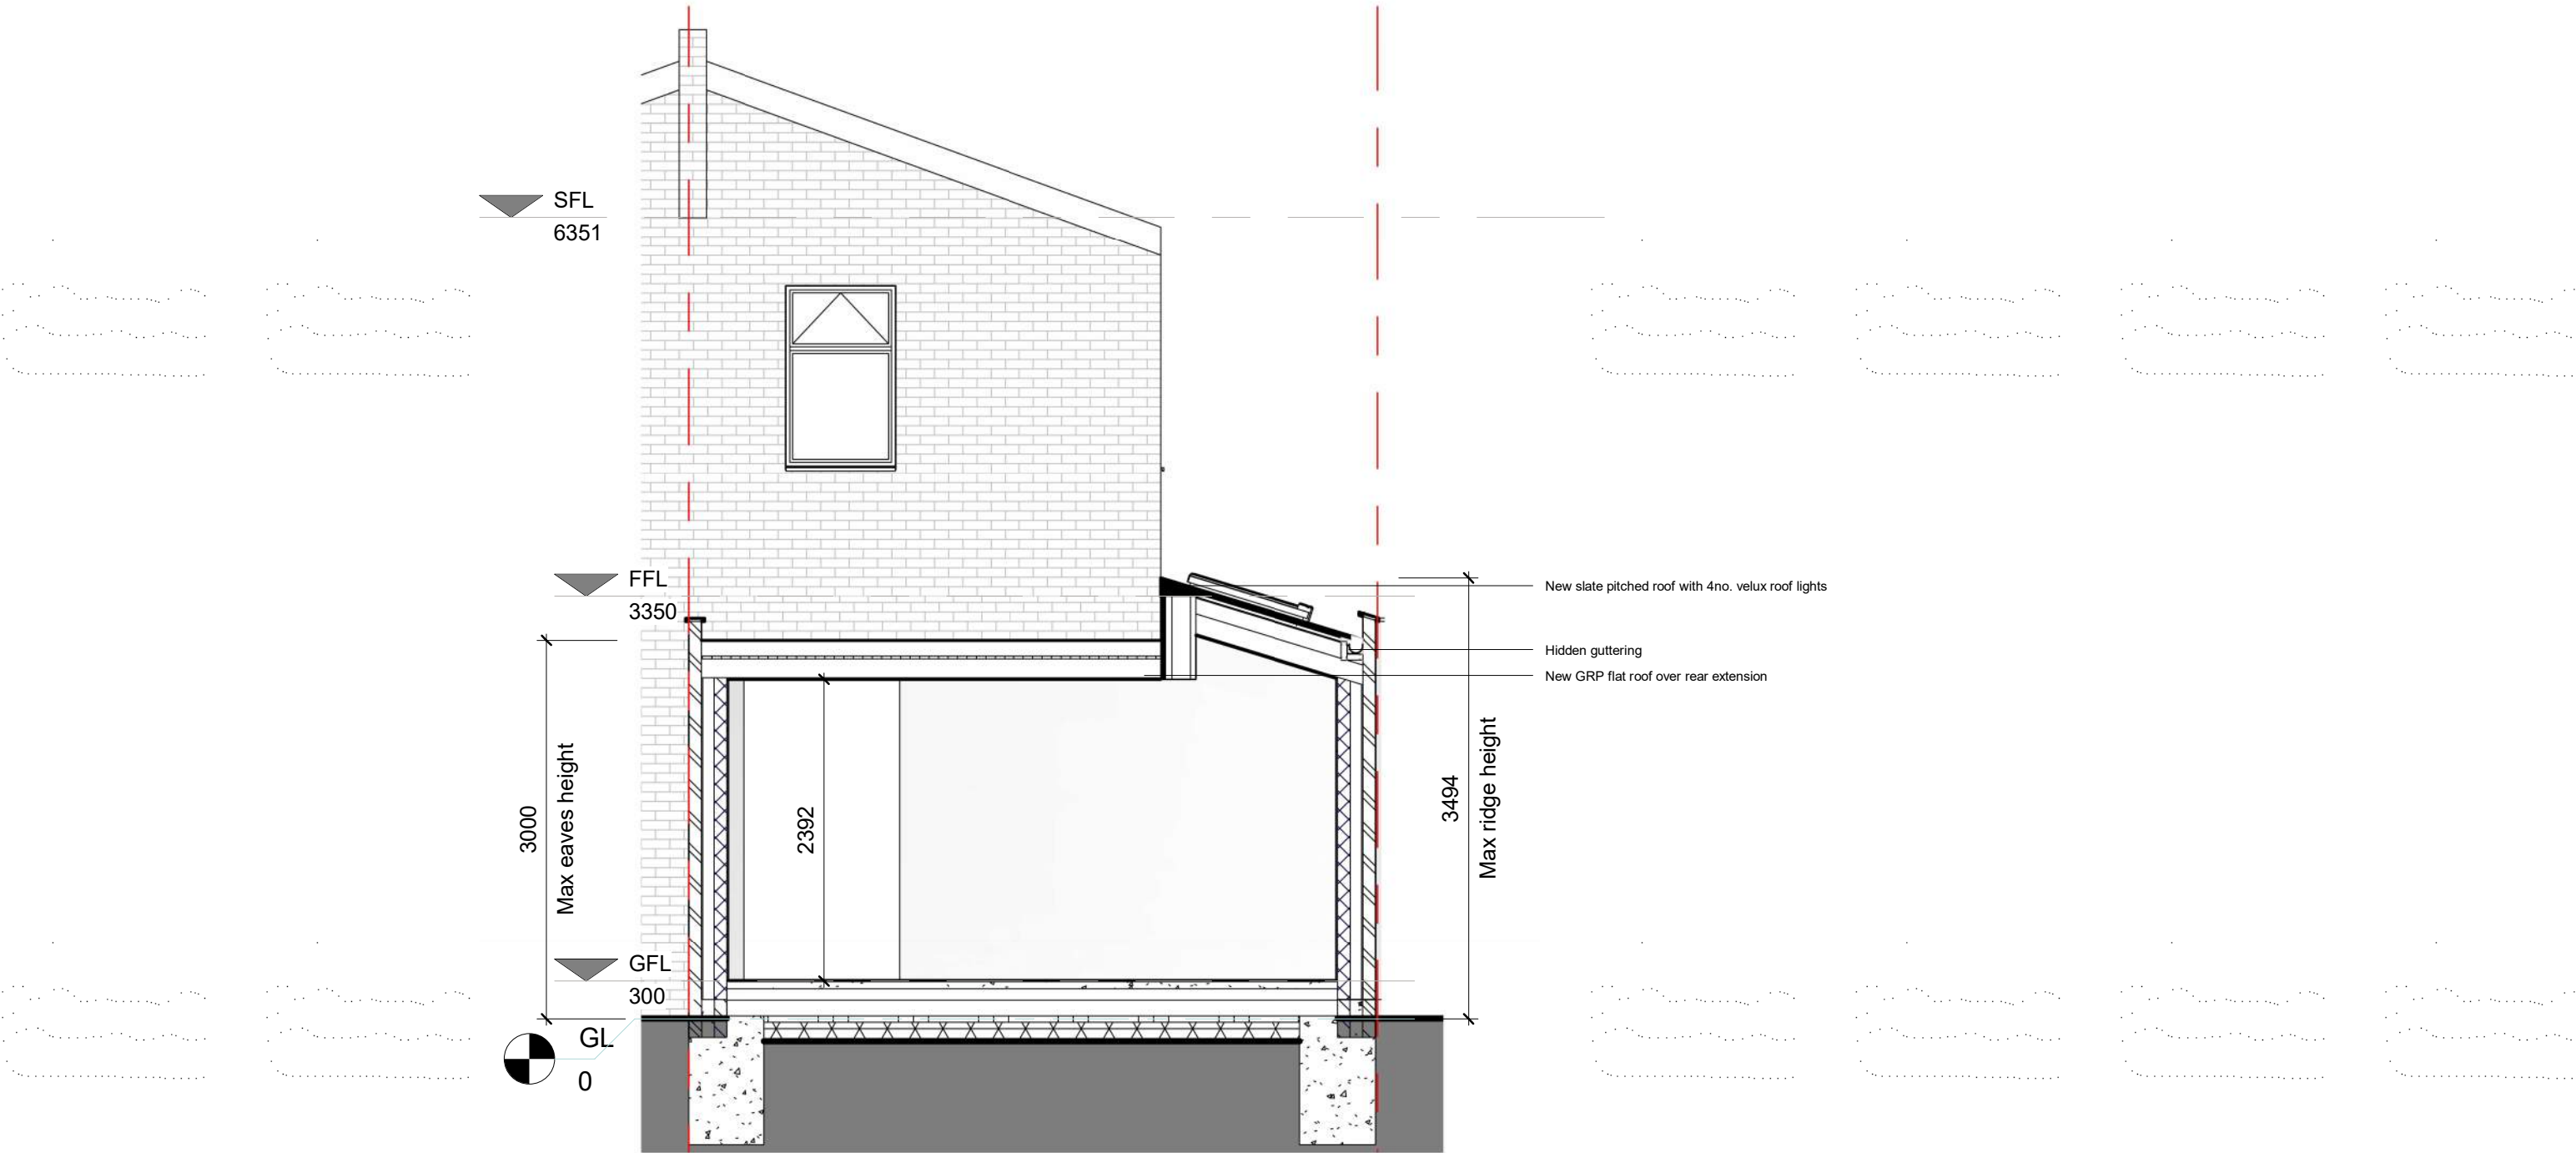

Boundary Section

1 : 50

NOTES:

TITLE:
Boundary Detail

SITE:
Alex Keating
107a Cavendish Road,
London,
SW12 0BN


PROJECT NO.
2024_11_SW12_KEA

SCALE AT A3 DRAWING NO. DATE.
1 : 50 A103 05/07/24

DRAWN. BY CHECKED. BY REVISION.

THE COPYRIGHT of this drawing is vested in Brunthan Yoheswaran and it may not be reproduced in whole or in part or used for the manufacture of any article without the express permission of the copyright holder.
THE SPECIFICATION in this drawing to be read in accordance with all relevant plans, elevations, sections and structural engineer's designs/calculations
ALL DIMENSIONS to be confirmed on site before the manufacture of any article
DO NOT SCALE off Drawing except for approximate dimensions
ALL WORKMANSHIP to be undertaken in strict accordance with the approval of the LPA Building Control Officer and in strict adherence with current British Standards and codes of practice
ALL MATERIALS used in construction or manufacture to be in strict adherence with current British Standards and codes of practice
ALL NEW GLAZING AND WINDOWS to meet thermal and ventilation requirements of current LPA Building Regulations
ELECTRICAL EQUIPMENT/WIRING: design & installation of all electrical wiring & related fittings to be carried out by an appd. electrical engineer in strict adherence to current British Standards and codes of practice
GAS/PLUMBING APPLIANCES: design & installation of all gas & plumbing & related fittings, appliances and equipment to be carried out by an appd. gas engineer in strict adherence to current British Standards and codes of practice

No	R.Desc	R.Date
----	--------	--------

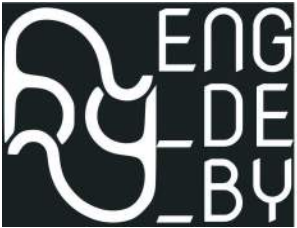

Planning &
Structural Engineering

info@engdeby.co.uk
+44 (0)7886 701 813